


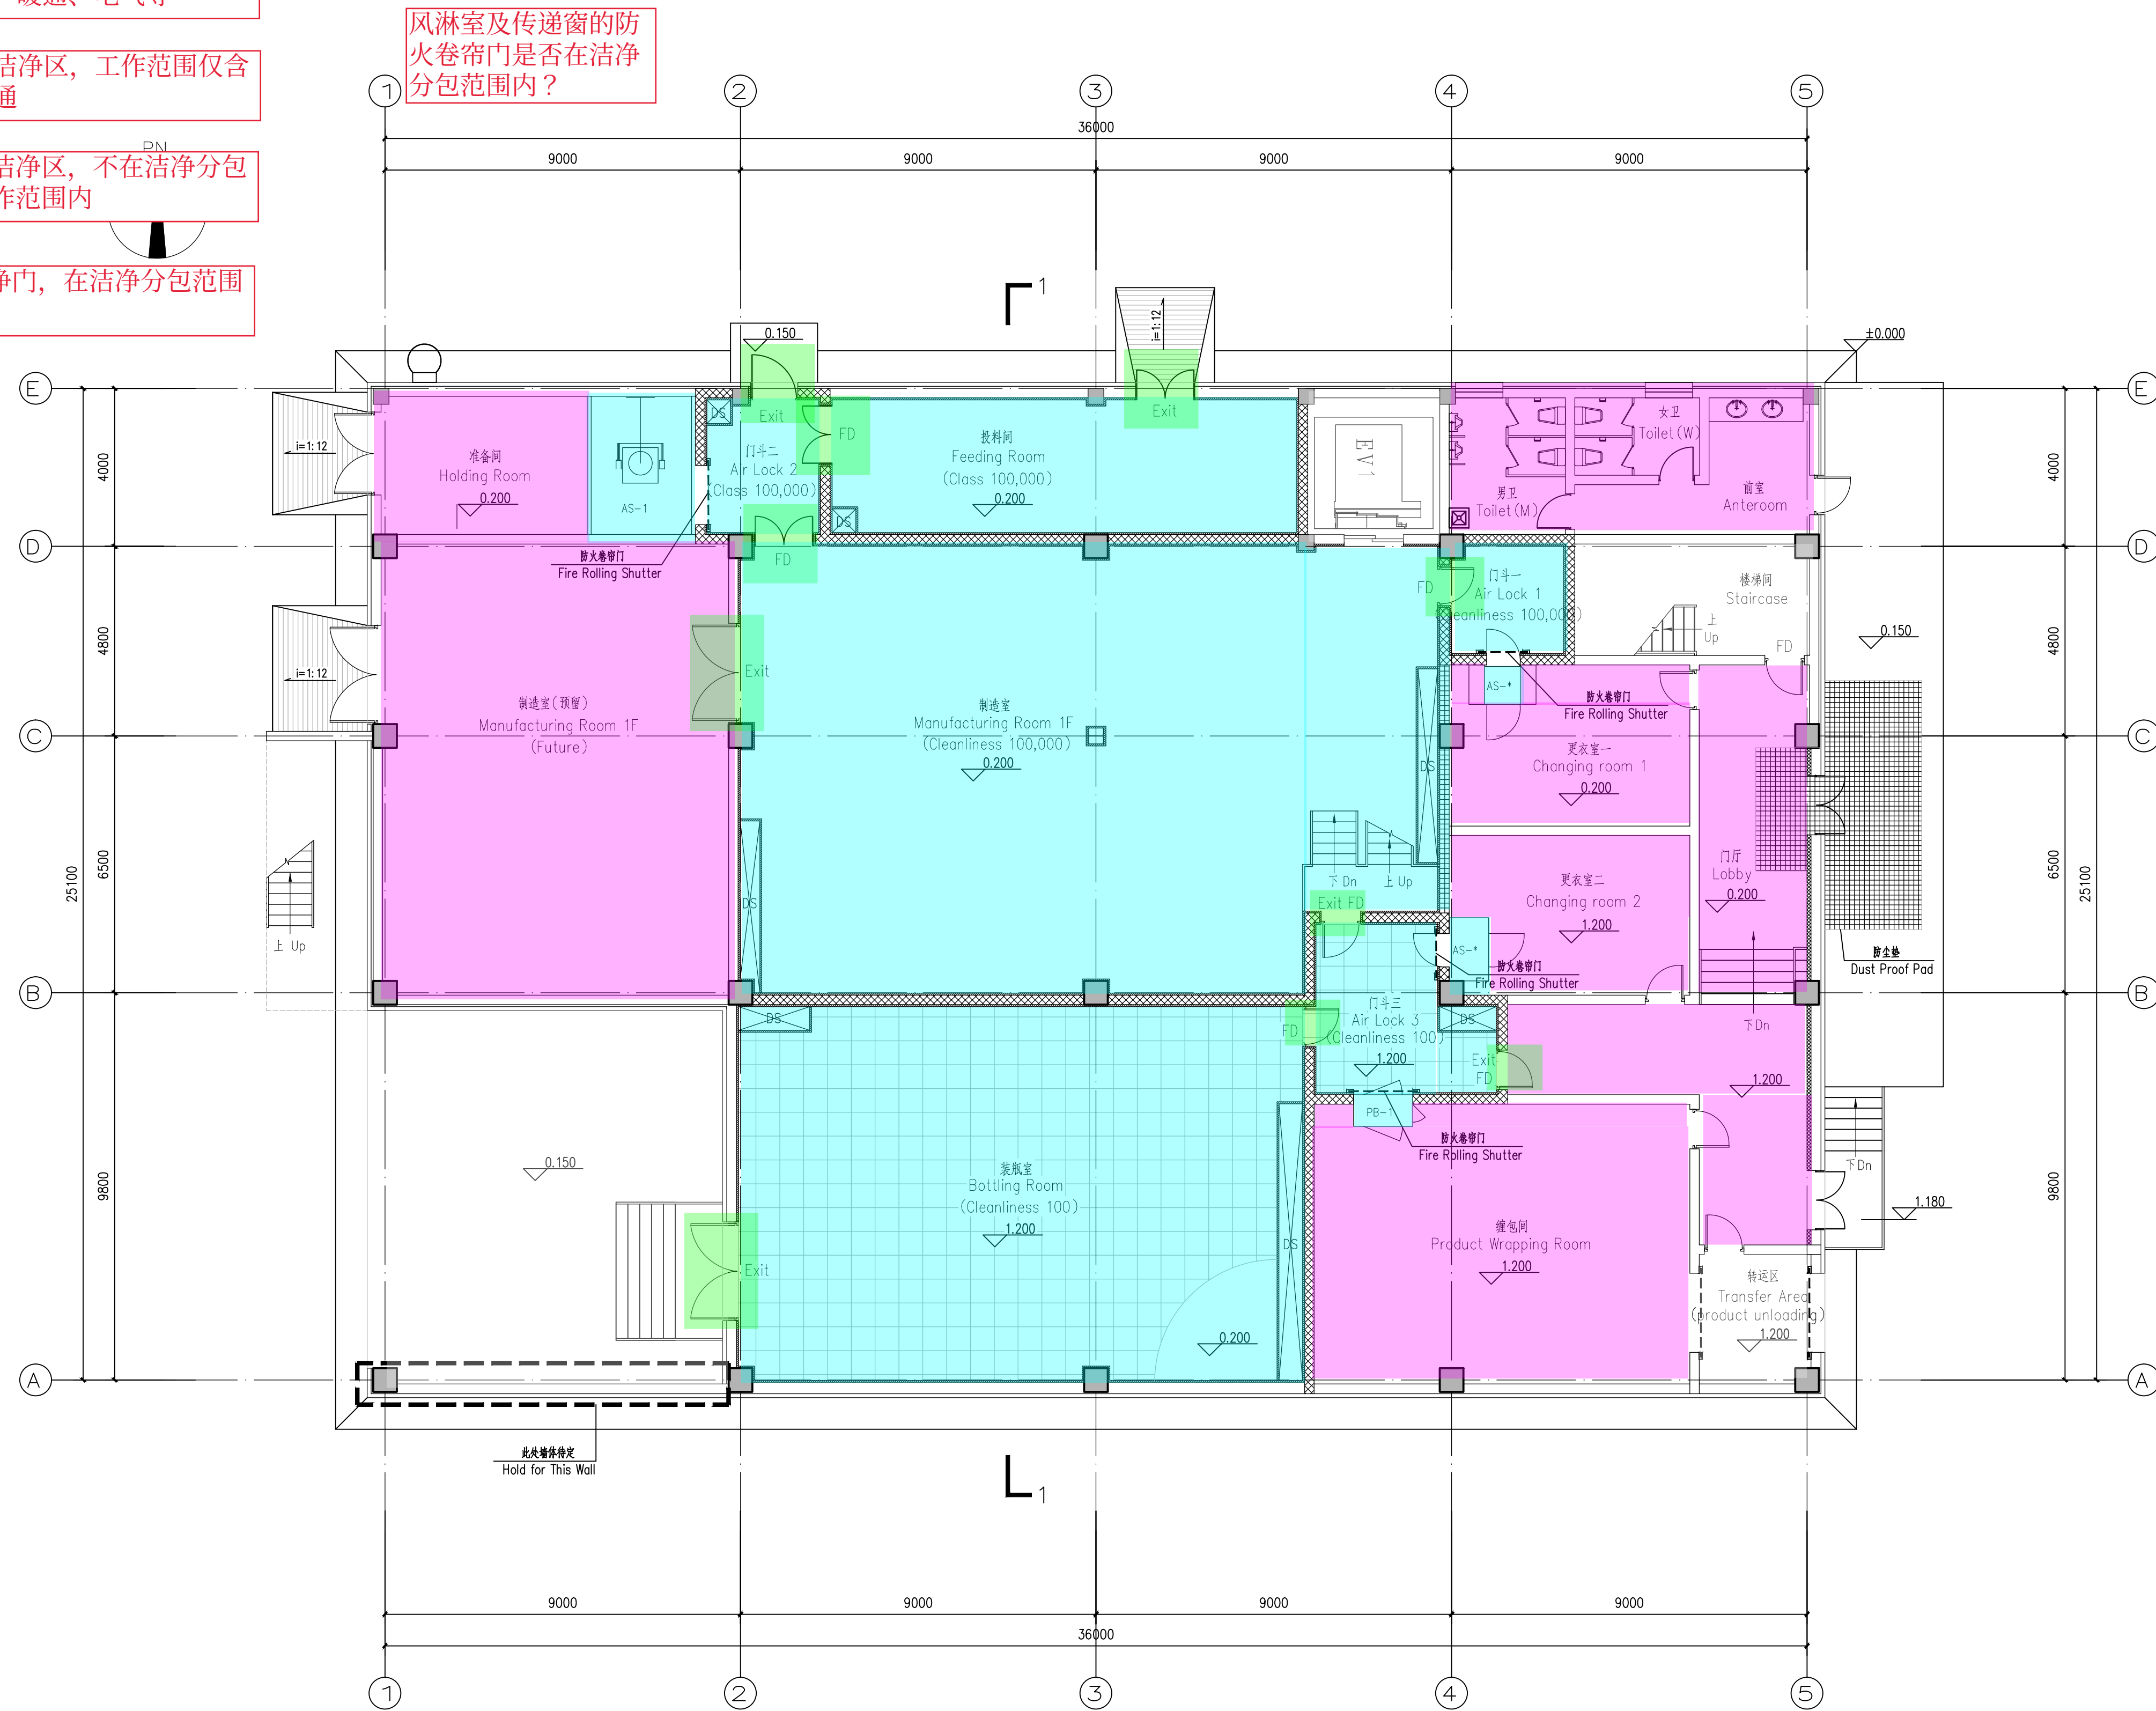


一层平面图  
First Floor Plan

|                           |                                                                                       |             |           |      |       |       |  |         |       |       |  |                                            |                                                                                       |
|---------------------------|---------------------------------------------------------------------------------------|-------------|-----------|------|-------|-------|--|---------|-------|-------|--|--------------------------------------------|---------------------------------------------------------------------------------------|
| SECURITY LEVEL<br>LEVEL-2 |  |             |           |      |       |       |  | DATE    |       | MADE  |  | TITLE                                      |                                                                                       |
|                           |  |             |           |      |       |       |  | SCALE   | 1/100 | CH*KD |  | Manufacturing Building<br>First Floor Plan |                                                                                       |
|                           |  |             |           |      |       |       |  | JOB No. |       | APP'D |  |                                            |                                                                                       |
|                           |  | BED PACKAGE | Apr 20/26 | LAY  | YN    | DN    |  |         |       |       |  |                                            |                                                                                       |
|                           | No.                                                                                   | DESCRIPTION | DATE      | MADE | CH*KD | APP'D |  |         |       |       |  | DWG. No.                                   | REV.                                                                                  |
|                           | REVISIONS                                                                             |             |           |      |       |       |  |         |       |       |  | ED-300-ARC-LAY-RCBG-0001                   |  |



- 洁净区，工作范围含土  
建、暖通、电气等
- 非洁净区，工作范围仅含  
暖通
- 非洁净区，不在洁净分包  
工作范围内
- 洁净门，在洁净分包范围  
内

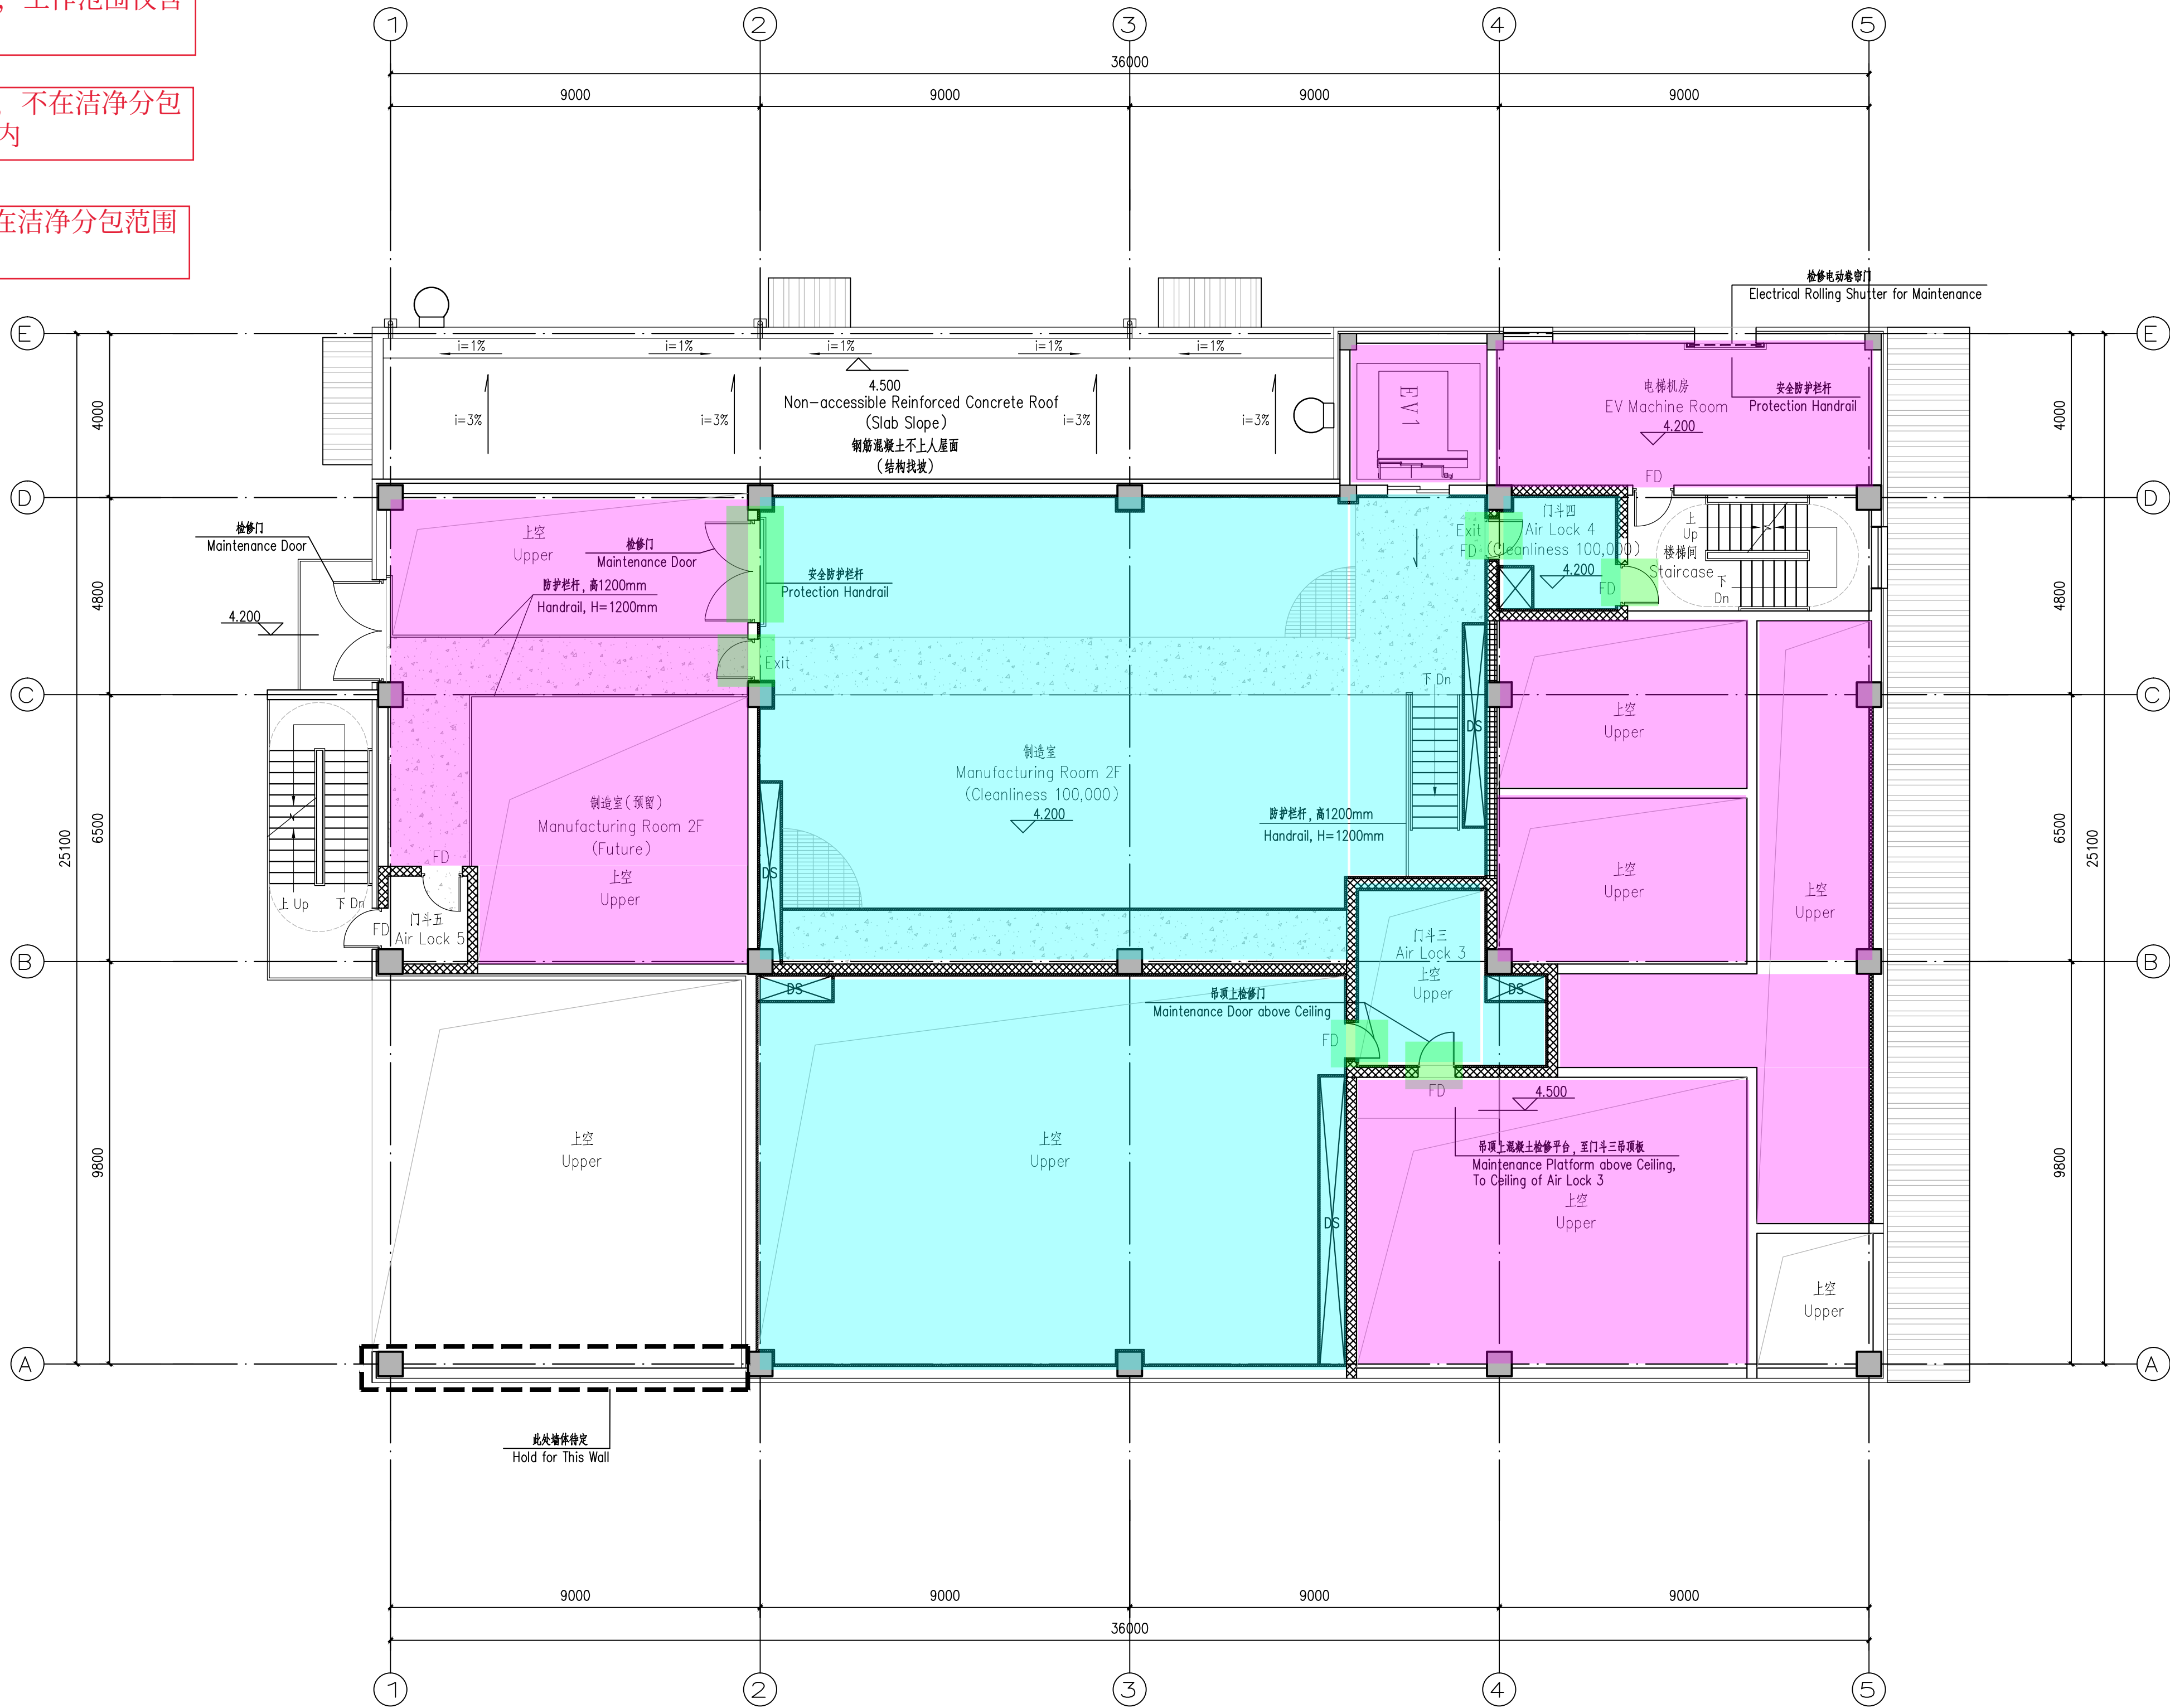

夹层平面图  
Mezzanine Floor Plan

1: 100

图例 Legend

100mm 成品金属岩棉夹芯板  
100mm Steel Sandwich Panel with Rock Wool

240厚蒸压加气混凝土砌块+ 方钢(见结构)  
+100mm 成品金属岩棉夹芯板  
240mm Aerated Concrete Block+Square Steel  
(refer to C/S Drawing)+100mm Steel Sandwich  
Panel with Rock Wool

240厚蒸压加气混凝土砌块  
240mm Aerated Concrete Block

防火隔墙，耐火极限不小于3h：240厚蒸压加气混凝土砌块  
Fire Partition Wall, Fire Resistance no less than 3h  
240mm Aerated Concrete Block

防爆防火隔墙，耐火极限不小于3h：  
240厚混凝土实心砖配筋  
Reinforced Fire Partition Wall,  
Fire Resistance no less than 3h  
240mm Reinforced Solid Concrete Brick

轻钢龙骨石膏板墙  
Gypsum Board

洁净板  
Clean Board

混凝土地坪，面层为环氧自流平  
Concrete Floor with Self-levelling Epoxy

不锈钢格栅(见结构图)  
Stainless Steel Grating (refer to C/S Drawing)

紧急疏散出口  
Emergency Evacuation

防火分区 Fire Compartment

1

5

E

E

1

5

A

A

防火分区一  
Fire Compartment I  
本层建筑面积420m<sup>2</sup>  
This Floor Area 420m<sup>2</sup>  
此防火分区面积1386m<sup>2</sup>  
Fire Compartment Area 1386m<sup>2</sup>



夹层平面图  
Mezzanine Floor Plan

|                           |             |  |  |      |           |                          |       |  |                        |
|---------------------------|-------------|--|--|------|-----------|--------------------------|-------|--|------------------------|
| △<br>△<br>△<br>△          |             |  |  |      | DATE      | 1/100                    | MAGE  |  | TITLE                  |
|                           |             |  |  |      | SCALE     | 1/100                    | CH·XD |  | Manufacturing Building |
|                           |             |  |  |      | JOB No.   |                          | APP·D |  | Mezzanine Floor Plan   |
|                           |             |  |  |      | DWG. No.  | ED-300-ARC-LAY-RCBG-0002 |       |  | REV.                   |
| SECURITY LEVEL<br>LEVEL-2 |             |  |  |      | REVISIONS |                          |       |  |                        |
| No.                       | DESCRIPTION |  |  | DATE | MADE      | CH·XD                    | APP·D |  |                        |


(A1)



- 洁净区，工作范围含土  
建、暖通、电气等
- 非洁净区，工作范围仅含  
暖通
- 非洁净区，不在洁净分包  
工作范围内
- 洁净门，在洁净分包范围  
内

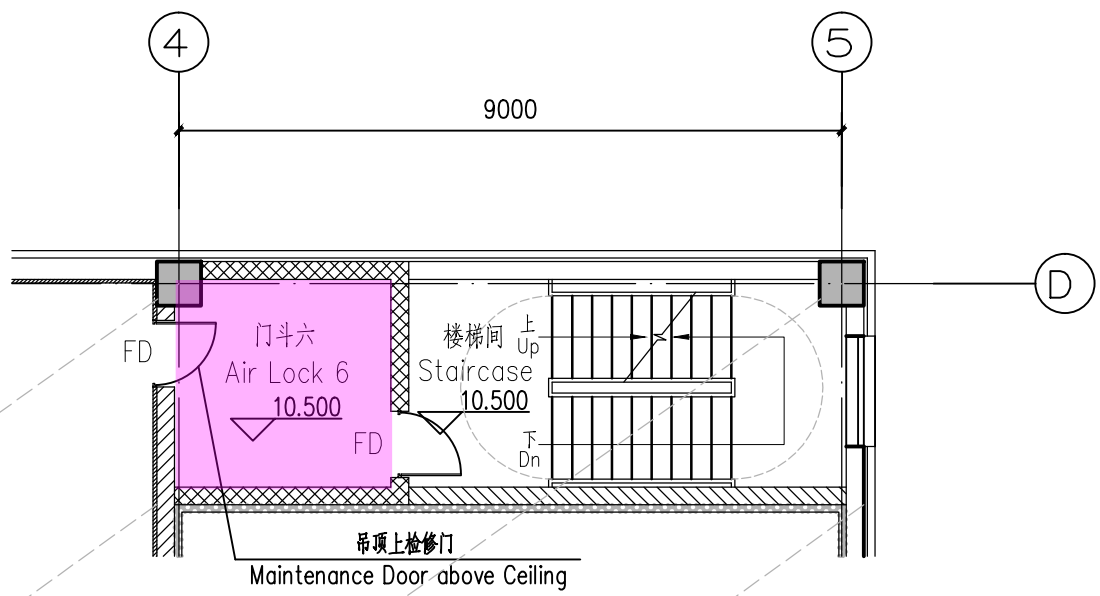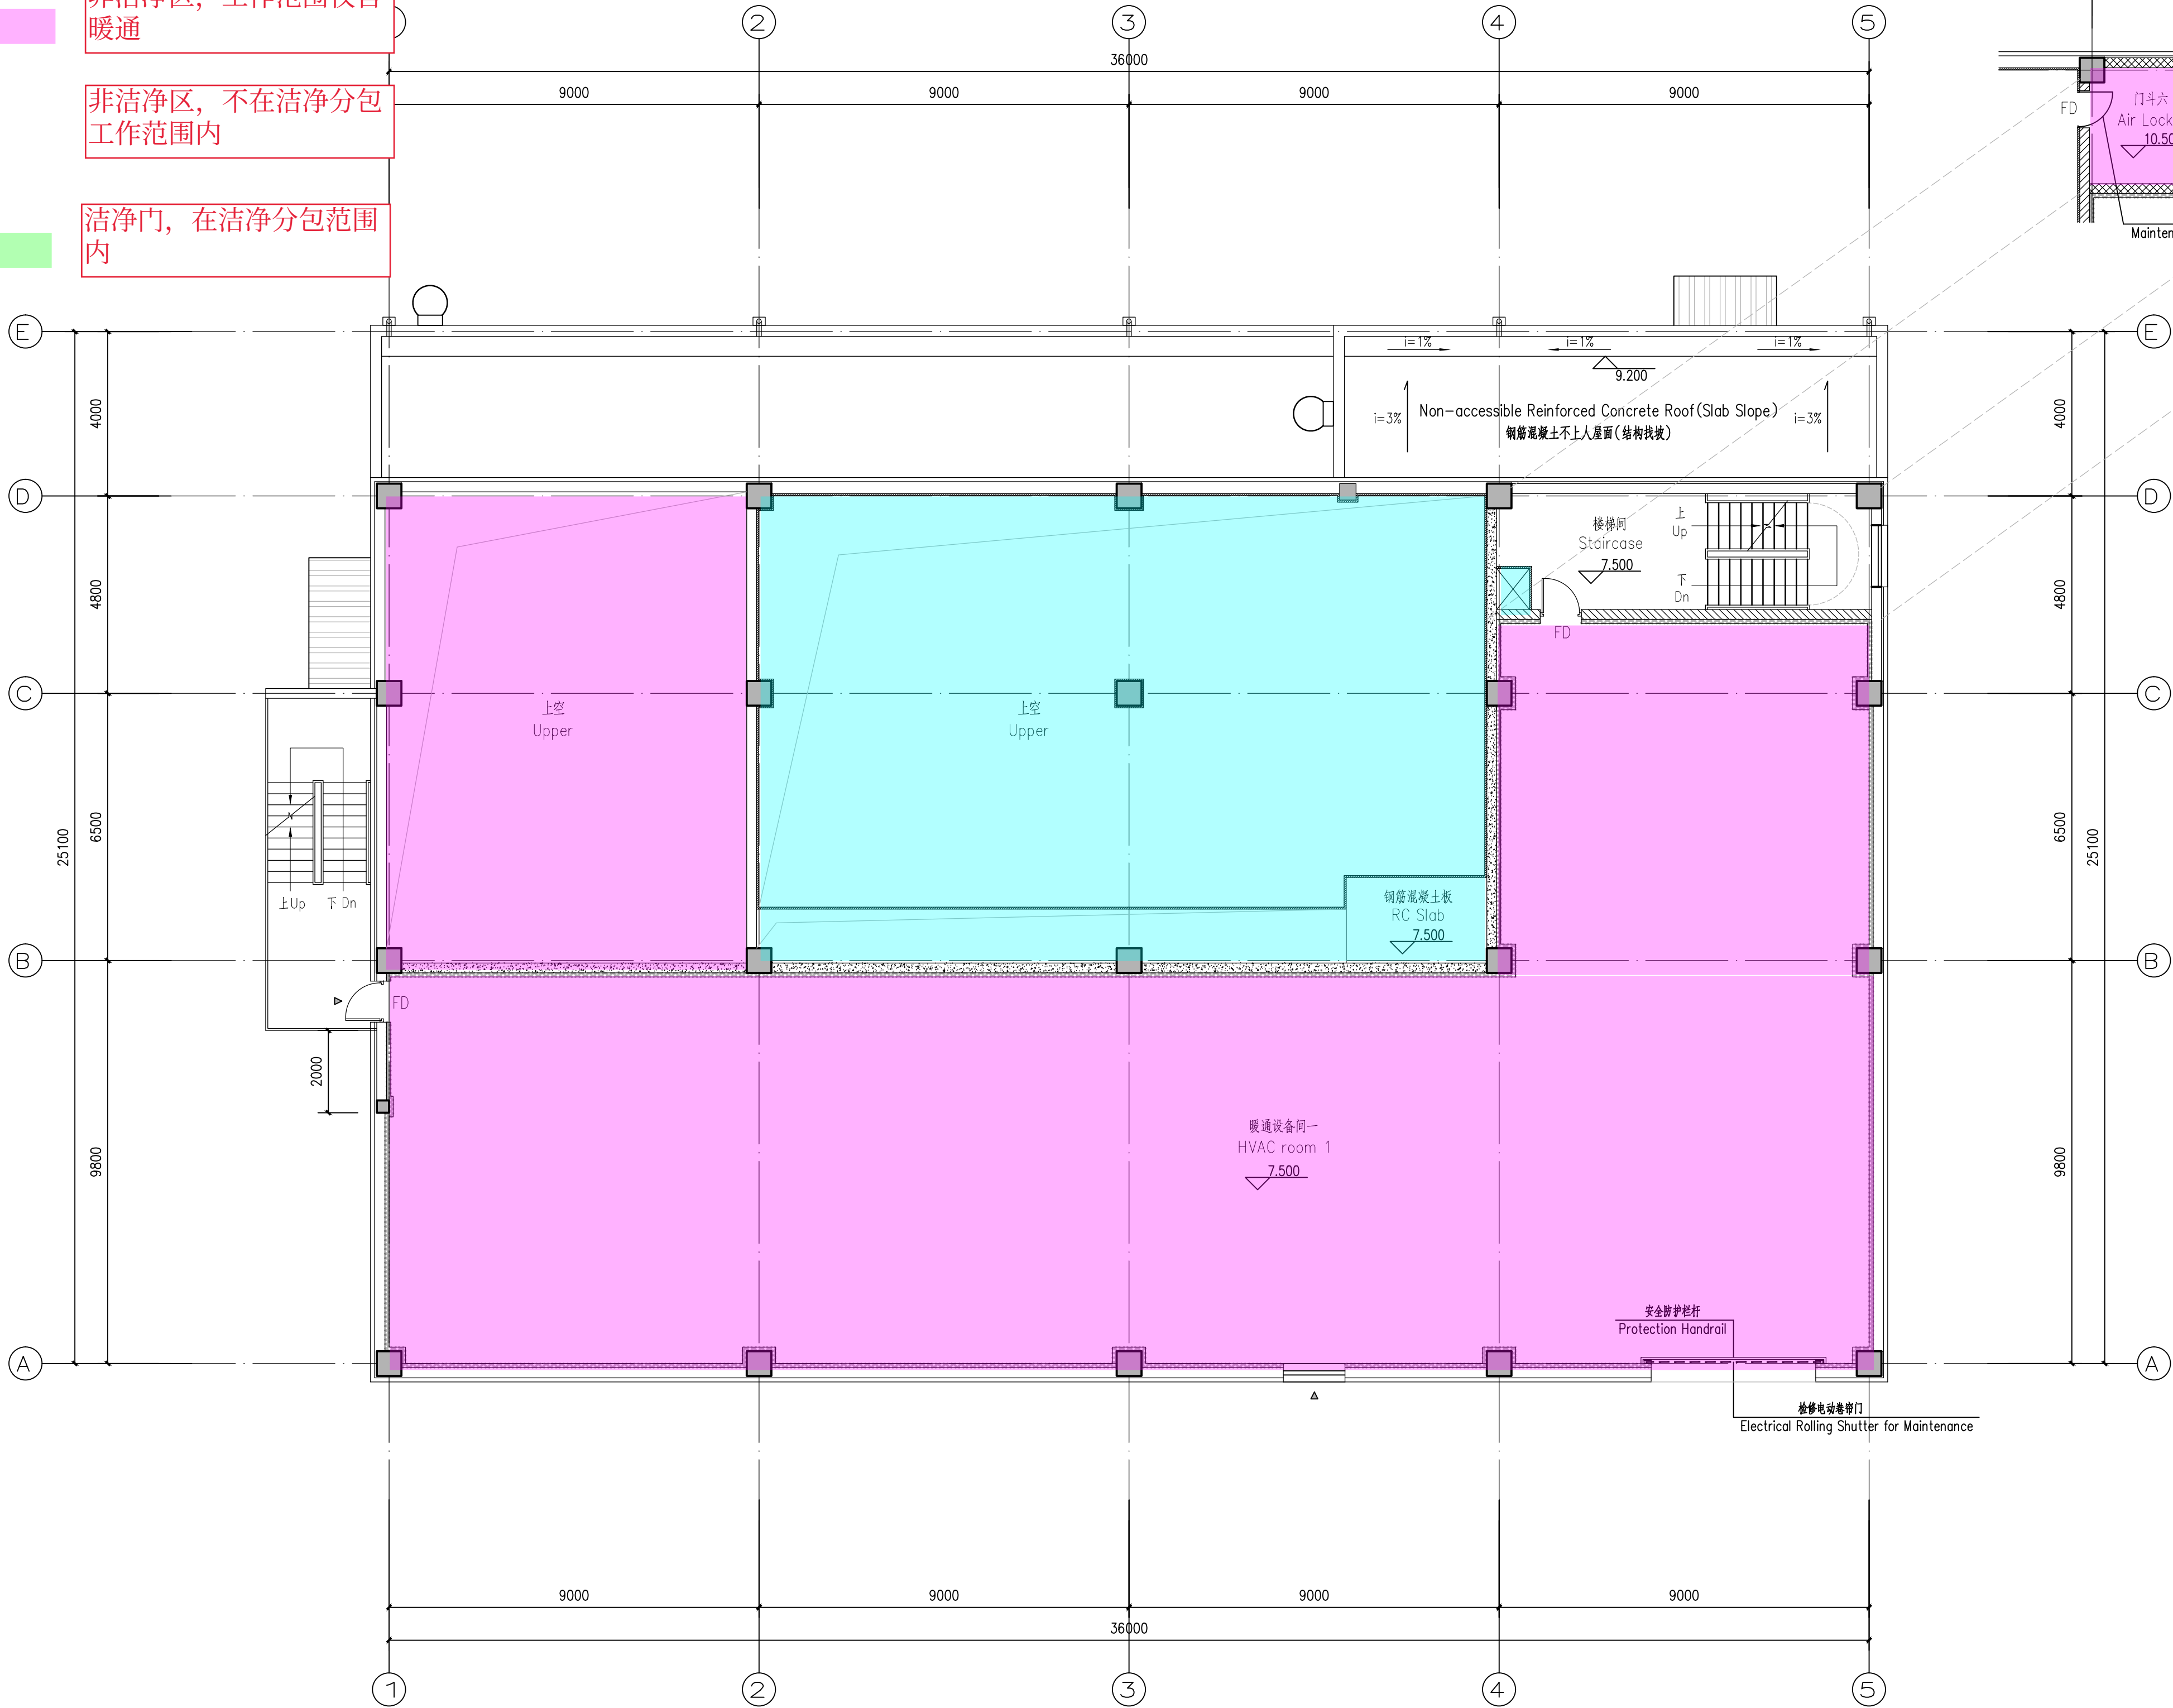

- 图例 Legend
- 100mm 成品金属岩棉夹芯板  
100mm Steel Sandwich Panel with Rock Wool
  - 240厚蒸压加气混凝土砌块+方钢(见结构)  
+100mm 成品金属岩棉夹芯板  
240mm Aerated Concrete Block+Square Steel  
(refer to C/S Drawing)+100mm Steel Sandwich  
Panel with Rock Wool
  - 240厚蒸压加气混凝土砌块  
240mm Aerated Concrete Block
  - 防火隔墙，耐火极限不小于3h：240厚蒸压加气混凝土砌块  
Fire Partition Wall, Fire Resistance no less than 3h  
240mm Aerated Concrete Block
  - 防火隔墙，耐火极限不小于2h：240厚蒸压加气混凝土砌块  
Fire Partition Wall, Fire Resistance no less than 2h  
240mm Aerated Concrete Block
  - 防爆防火墙，耐火极限不小于4h：  
240厚混凝土实心砖配筋  
Reinforced Fire Wall, Fire Resistance no less than 4h  
240mm Reinforced Solid Concrete Brick
  - 穿孔吸音石膏板内填玻璃棉  
Perforated Acoustic Gypsum Board with Glass Wool
  - 洁净板  
Clean Board
  - 消防接口  
Firefighting Opening

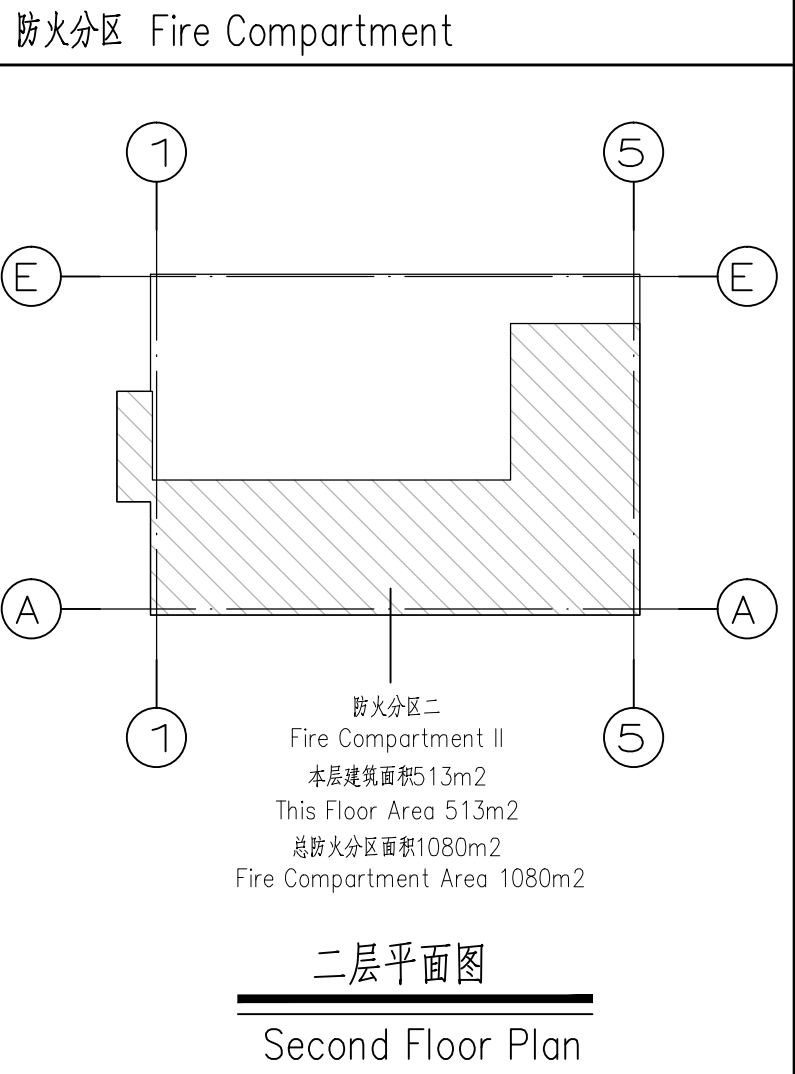


二层平面图  
Second Floor Plan 1: 100

|                                        |             |             |      |      |           |       |       |    |   |
|----------------------------------------|-------------|-------------|------|------|-----------|-------|-------|----|---|
| <div>△</div> <div>△</div> <div>△</div> |             |             |      |      | DATE      |       | MADE  |    | TITLE<br>Manufacturing Building<br>Second Floor Plan<br>DWG. No.<br>ED-300-ARC-LAY-RCBG-0003<br><div>△</div> |
|                                        |             |             |      |      | SCALE     | 1/100 | CH*XD |    |   |
|                                        | BED PACKAGE |             |      |      | Apr/20/26 | L*Y   | YN    | DH |   |
|                                        |             |             |      |      | JOB No.   |       | APP*D |    |   |
| SECURITY LEVEL<br>LEVEL-2              | No.         | DESCRIPTION | DATE | MADE | CH*XD     | APP*D |       |    |   |
| REVISIONS                              |             |             |      |      |           |       |       |    |   |




- 洁净区，工作范围含土  
建、暖通、电气等
- 非洁净区，工作范围仅含  
暖通
- 非洁净区，不在洁净分包  
工作范围内
- 洁净门，在洁净分包范围  
内

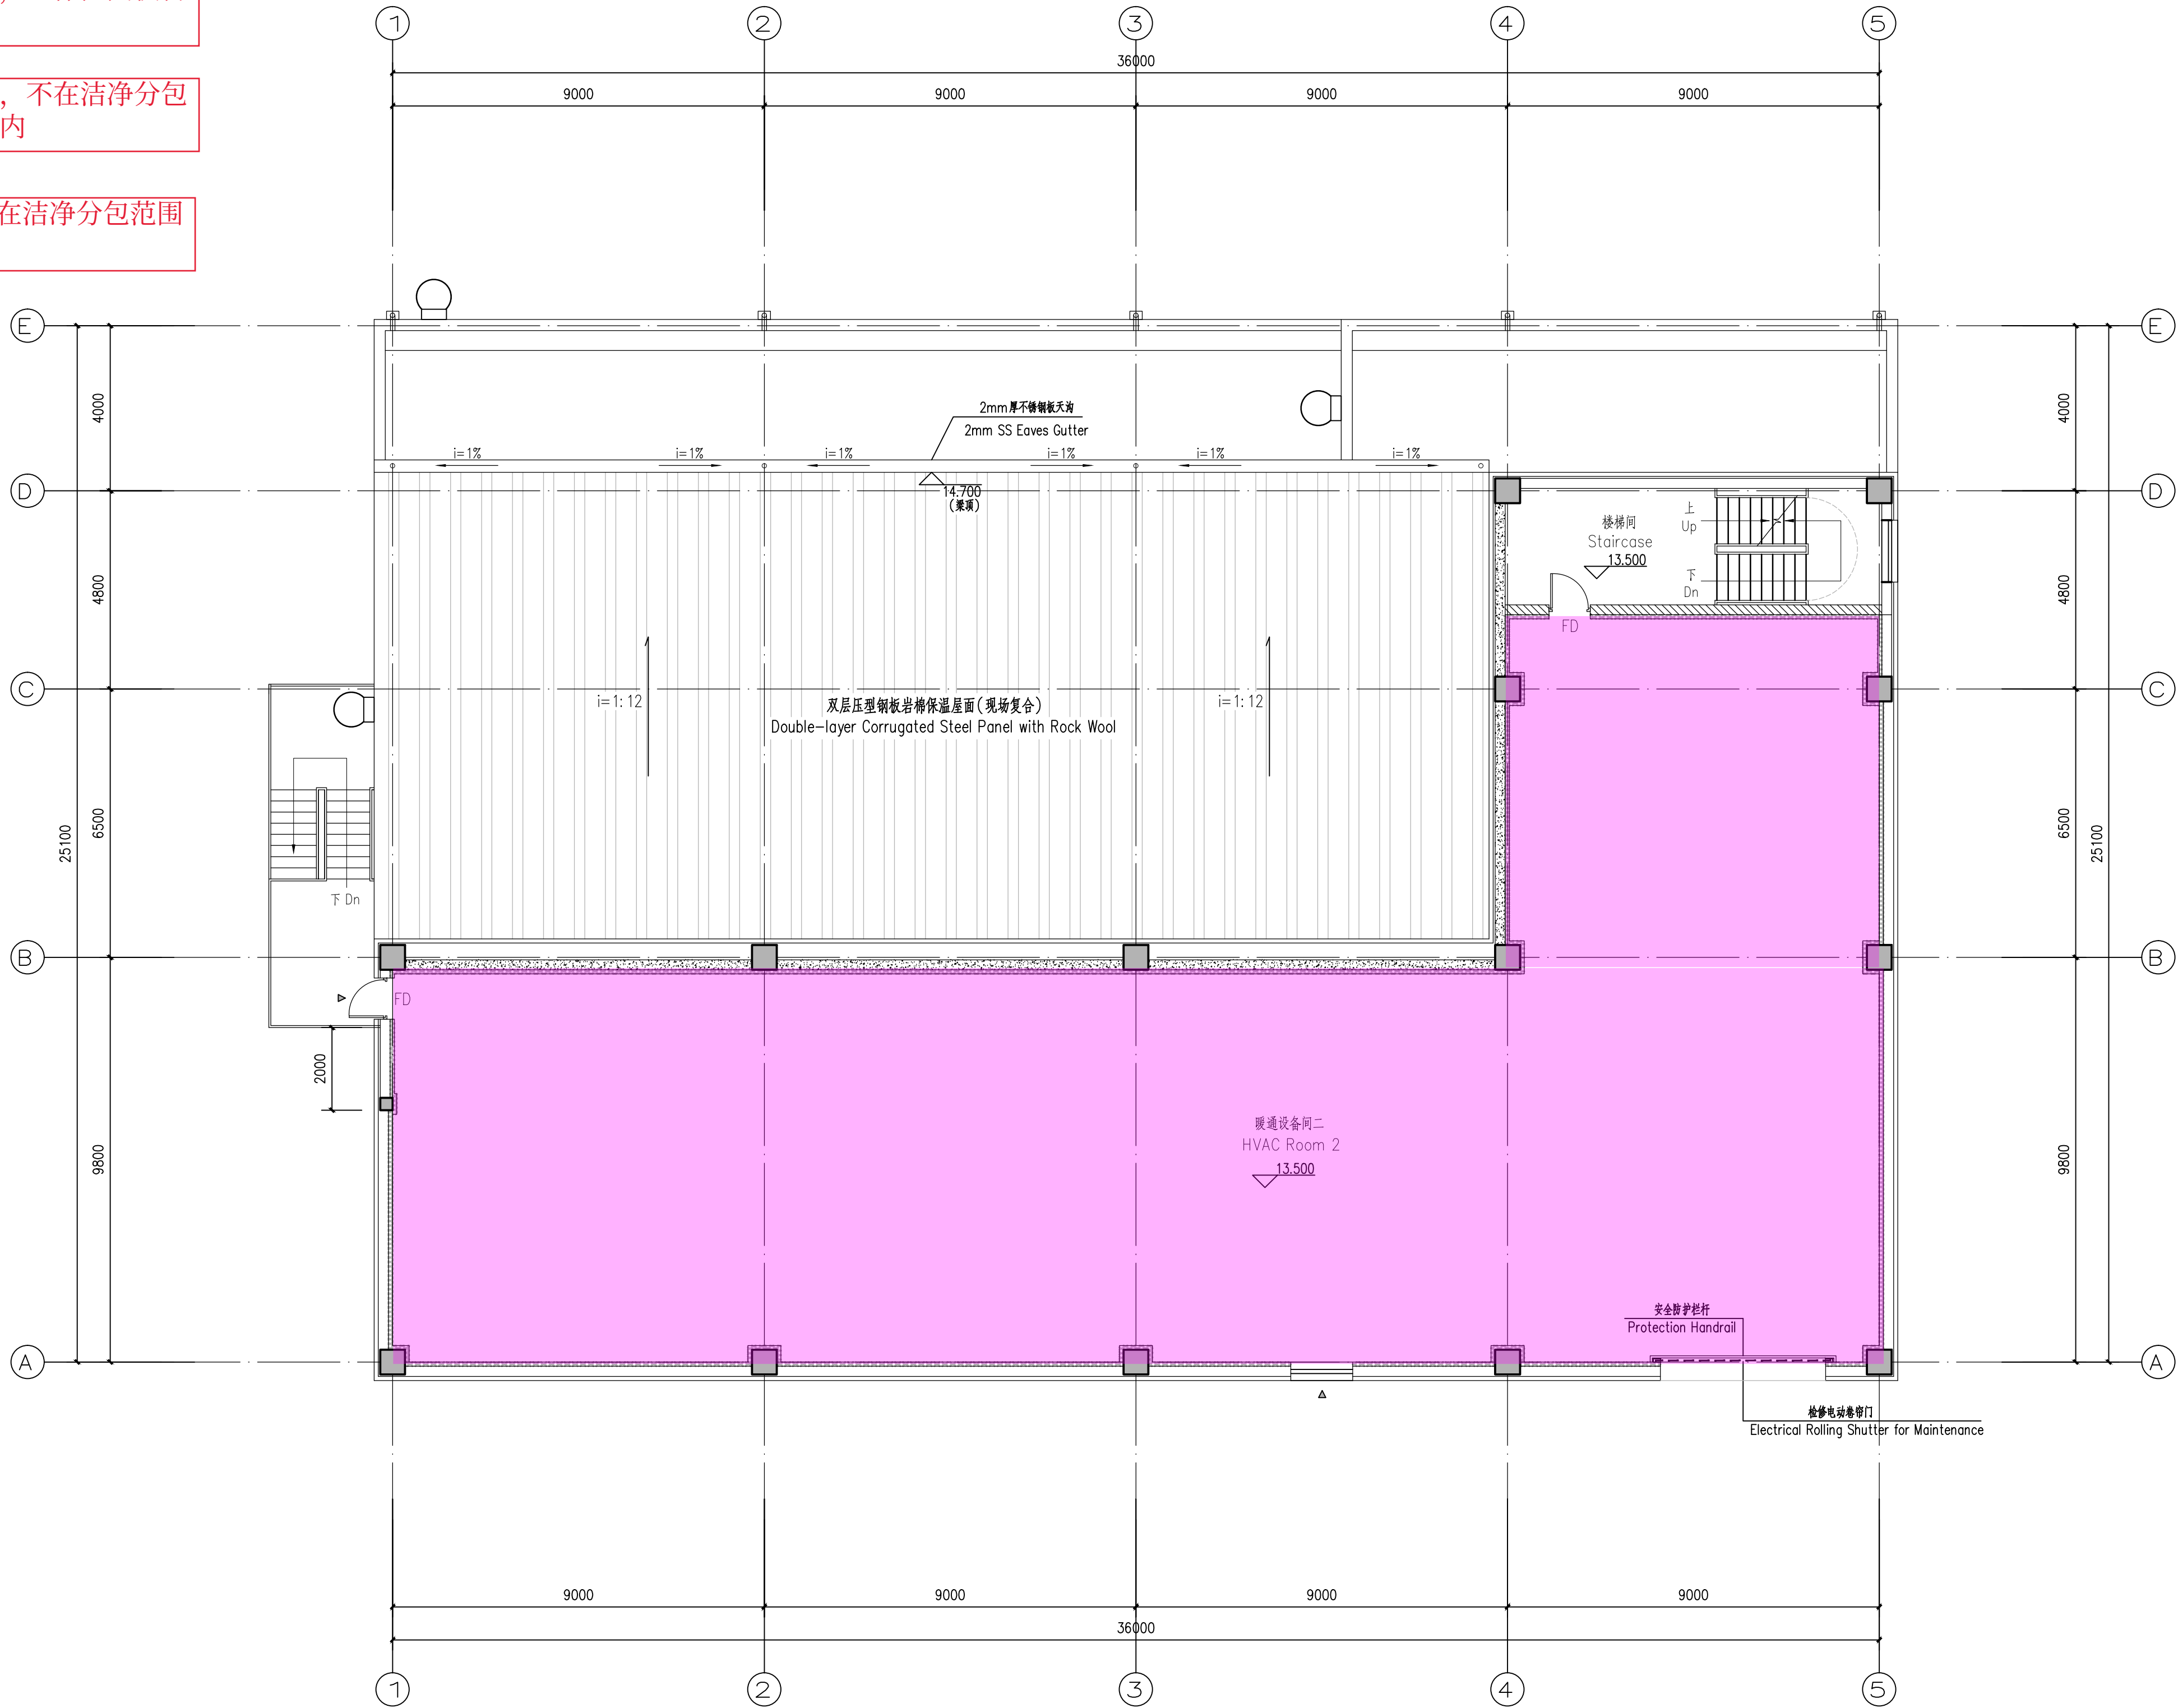

三层平面图  
Third Floor Plan 1:100


- 图例 Legend
- 100mm 成品金属岩棉夹芯板  
100mm Steel Sandwich Panel with Rock Wool
  - 240厚蒸压加气混凝土砌块+方钢 (见结构)  
+100mm 成品金属岩棉夹芯板  
240mm Aerated Concrete Block+Square Steel  
(refer to C/S Drawing)+100mm Steel Sandwich  
Panel with Rock Wool
  - 240厚蒸压加气混凝土砌块  
240mm Aerated Concrete Block
  - 防火隔墙，耐火极限不小于2h：240厚蒸压加气混凝土砌块  
Fire Partition Wall, Fire Resistance no less than 2h  
240mm Aerated Concrete Block
  - 防爆防火墙，耐火极限不小于4h：  
240厚混凝土实心砖配筋  
Reinforced Fire Wall, Fire Resistance no less than 4h  
240mm Reinforced Solid Concrete Brick
  - 穿孔吸音石膏板内填玻璃棉  
Perforated Acoustic Gypsum Board with Glass Wool
  - 消防接口  
Firefighting Opening

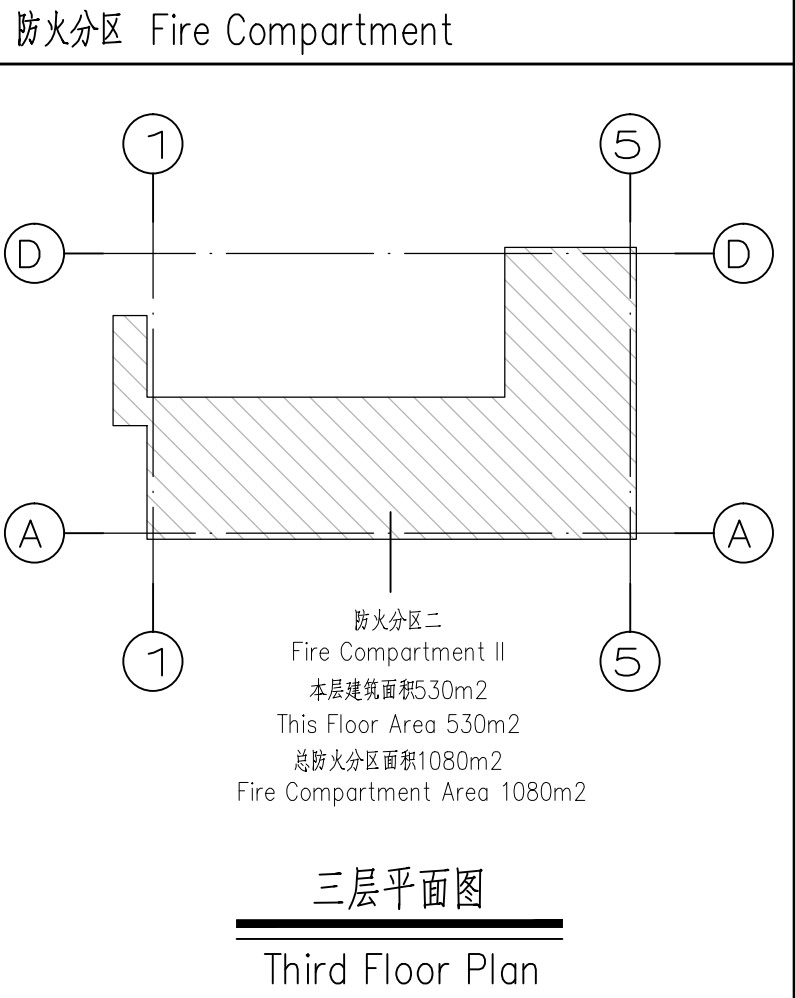

|                           |     |             |           |      |       |       |         |       |       |  |                                                         |                                      |           |
|---------------------------|-----|-------------|-----------|------|-------|-------|---------|-------|-------|--|---------------------------------------------------------|--------------------------------------|-----------|
|                           | △   |             |           |      |       |       | DATE    |       | MADE  |  | TITLE<br><br>Manufacturing Building<br>Third Floor Plan |                                      |           |
|                           | △   |             |           |      |       |       | SCALE   | 1/100 | CH·XD |  |                                                         |                                      |           |
|                           | △   |             |           |      |       |       | JOB No. |       | APP·D |  |                                                         |                                      |           |
|                           | △   | RED PACKAGE | Apr/20/26 | L·JY | YN    | DH    |         |       |       |  |                                                         |                                      |           |
| SECURITY LEVEL<br>LEVEL-2 | No. | DESCRIPTION | DATE      | MADE | CH·XD | APP·D |         |       |       |  |                                                         | DWG. No.<br>ED-300-ARC-LAY-RCBG-0004 | REV.<br>△ |
| REVISIONS                 |     |             |           |      |       |       |         |       |       |  |                                                         |                                      |           |




- 洁净区，工作范围含土  
建、暖通、电气等
- 非洁净区，工作范围仅含  
暖通
- 非洁净区，不在洁净分包  
工作范围内
- 洁净门，在洁净分包范围  
内

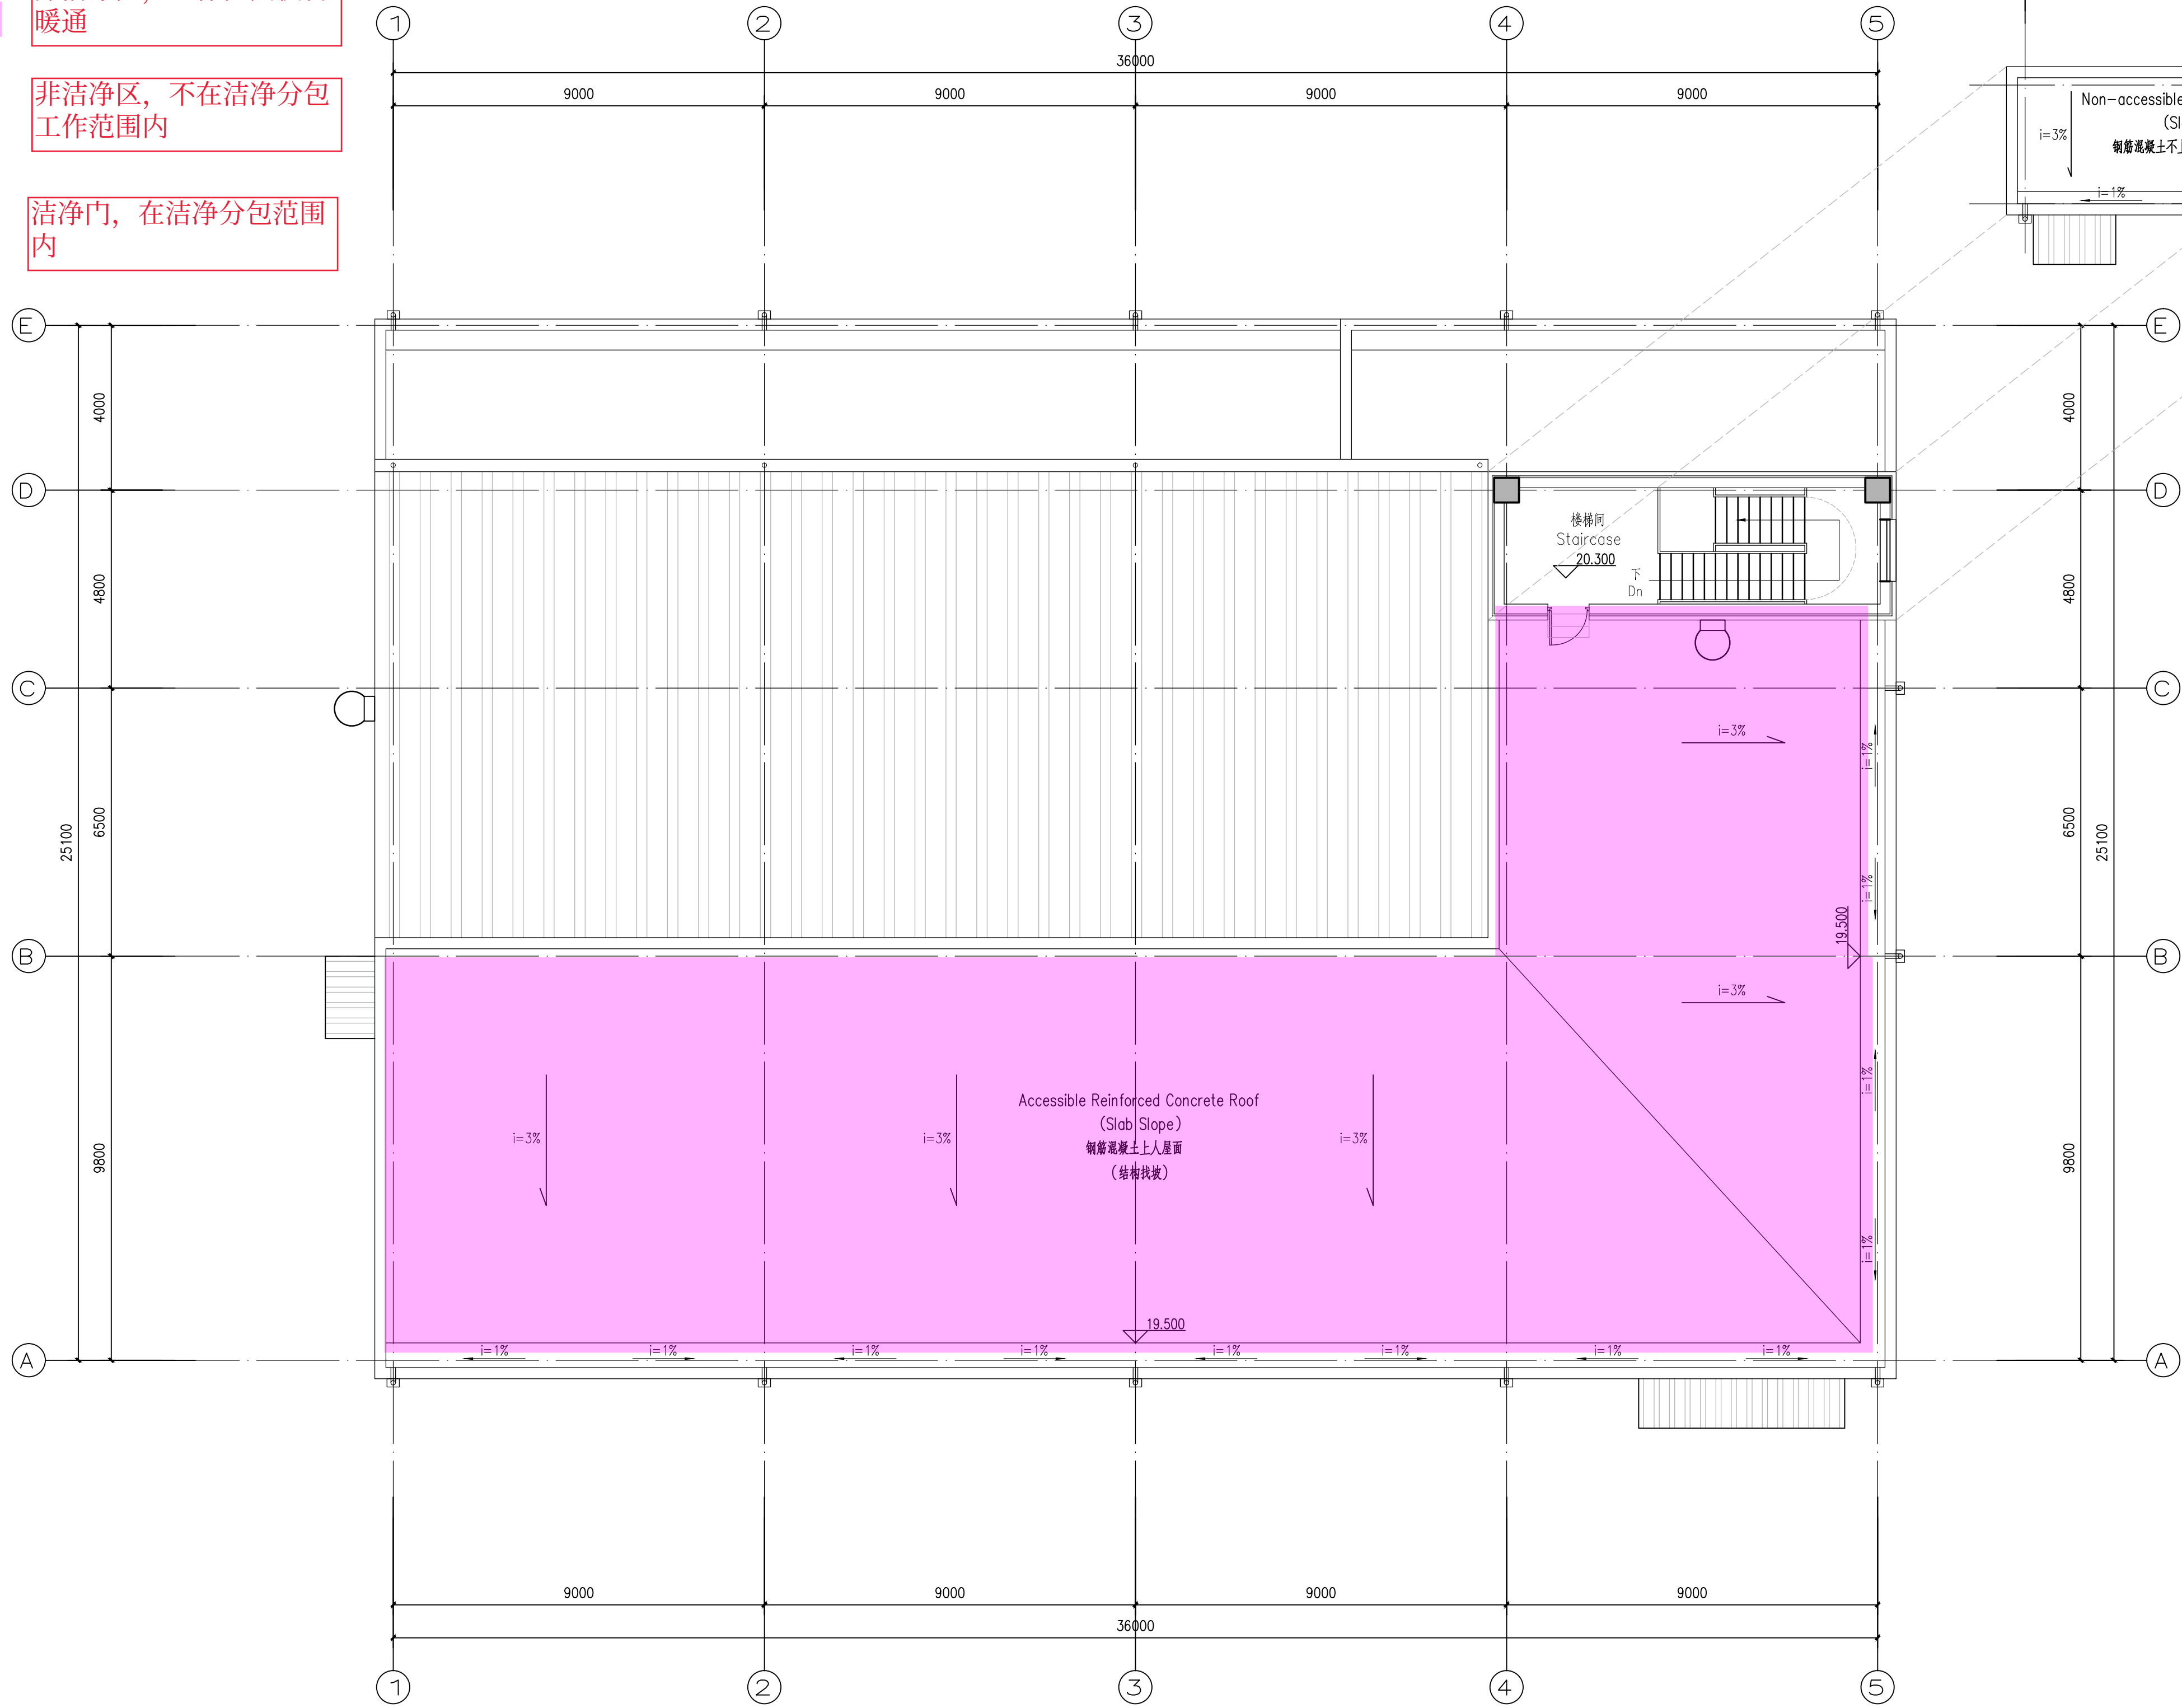

屋顶平面图  
Roof Plan


1: 100

- 图例 Legend
- 240厚蒸压加气混凝土砌块+方钢(见结构)  
+100mm 成品金属岩棉夹芯板  
240mm Aerated Concrete Block+Square Steel  
(refer to C/S Drawing)+100mm Steel Sandwich  
Panel with Rock Wool

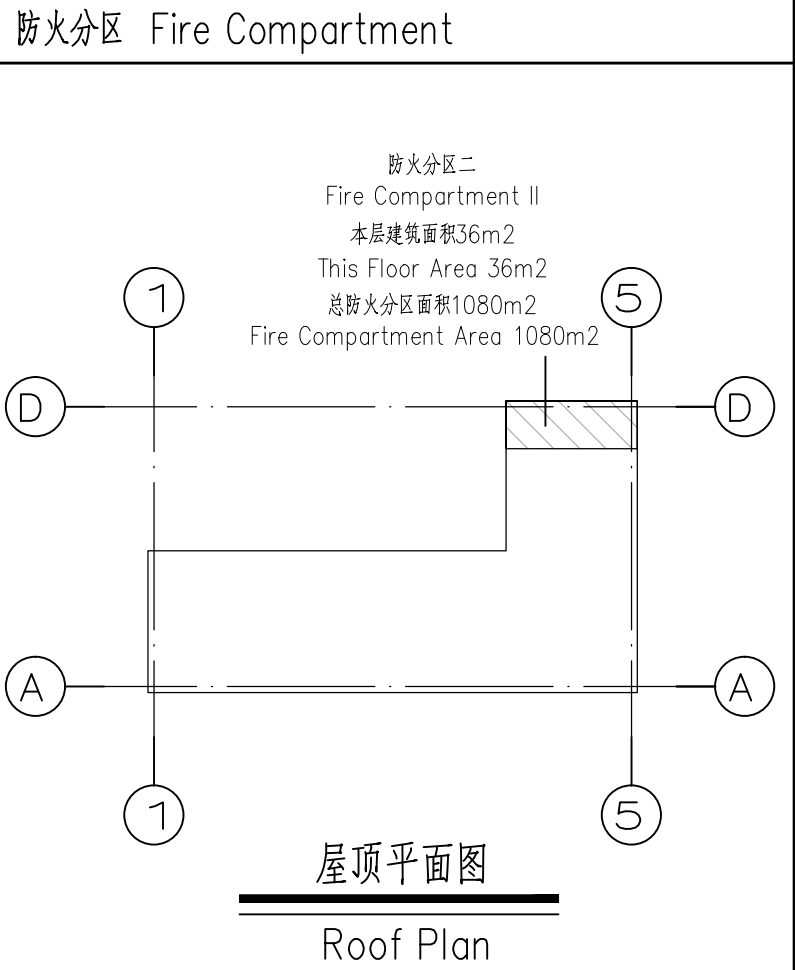

|                                                         |             |             |      |      |       |         |           |       |  |                                                                                      |                                |
|---------------------------------------------------------|-------------|-------------|------|------|-------|---------|-----------|-------|--|--------------------------------------------------------------------------------------|--------------------------------|
| <div><div></div><div></div><div></div><div></div></div> |             |             |      |      |       | DATE    |           | MADE  |  | TITLE<br>Manufacturing Building<br>Roof Plan<br>DWG. No.<br>ED-300-ARC-LAY-RCBG-0005 |                                |
|                                                         |             |             |      |      |       | SCALE   | 1/100     | CH·XD |  |                                                                                      |                                |
|                                                         | RED PACKAGE |             |      |      |       | JOB No. |           | APP·D |  |                                                                                      |                                |
|                                                         | Apr/20/26   |             |      |      |       | L·Y     | Y·N       | D·H   |  |                                                                                      |                                |
| SECURITY LEVEL<br>LEVEL-2                               | No.         | DESCRIPTION | DATE | MADE | CH·XD | APP·D   | REVISIONS |       |  |                                                                                      | REV.<br><div><div></div></div> |




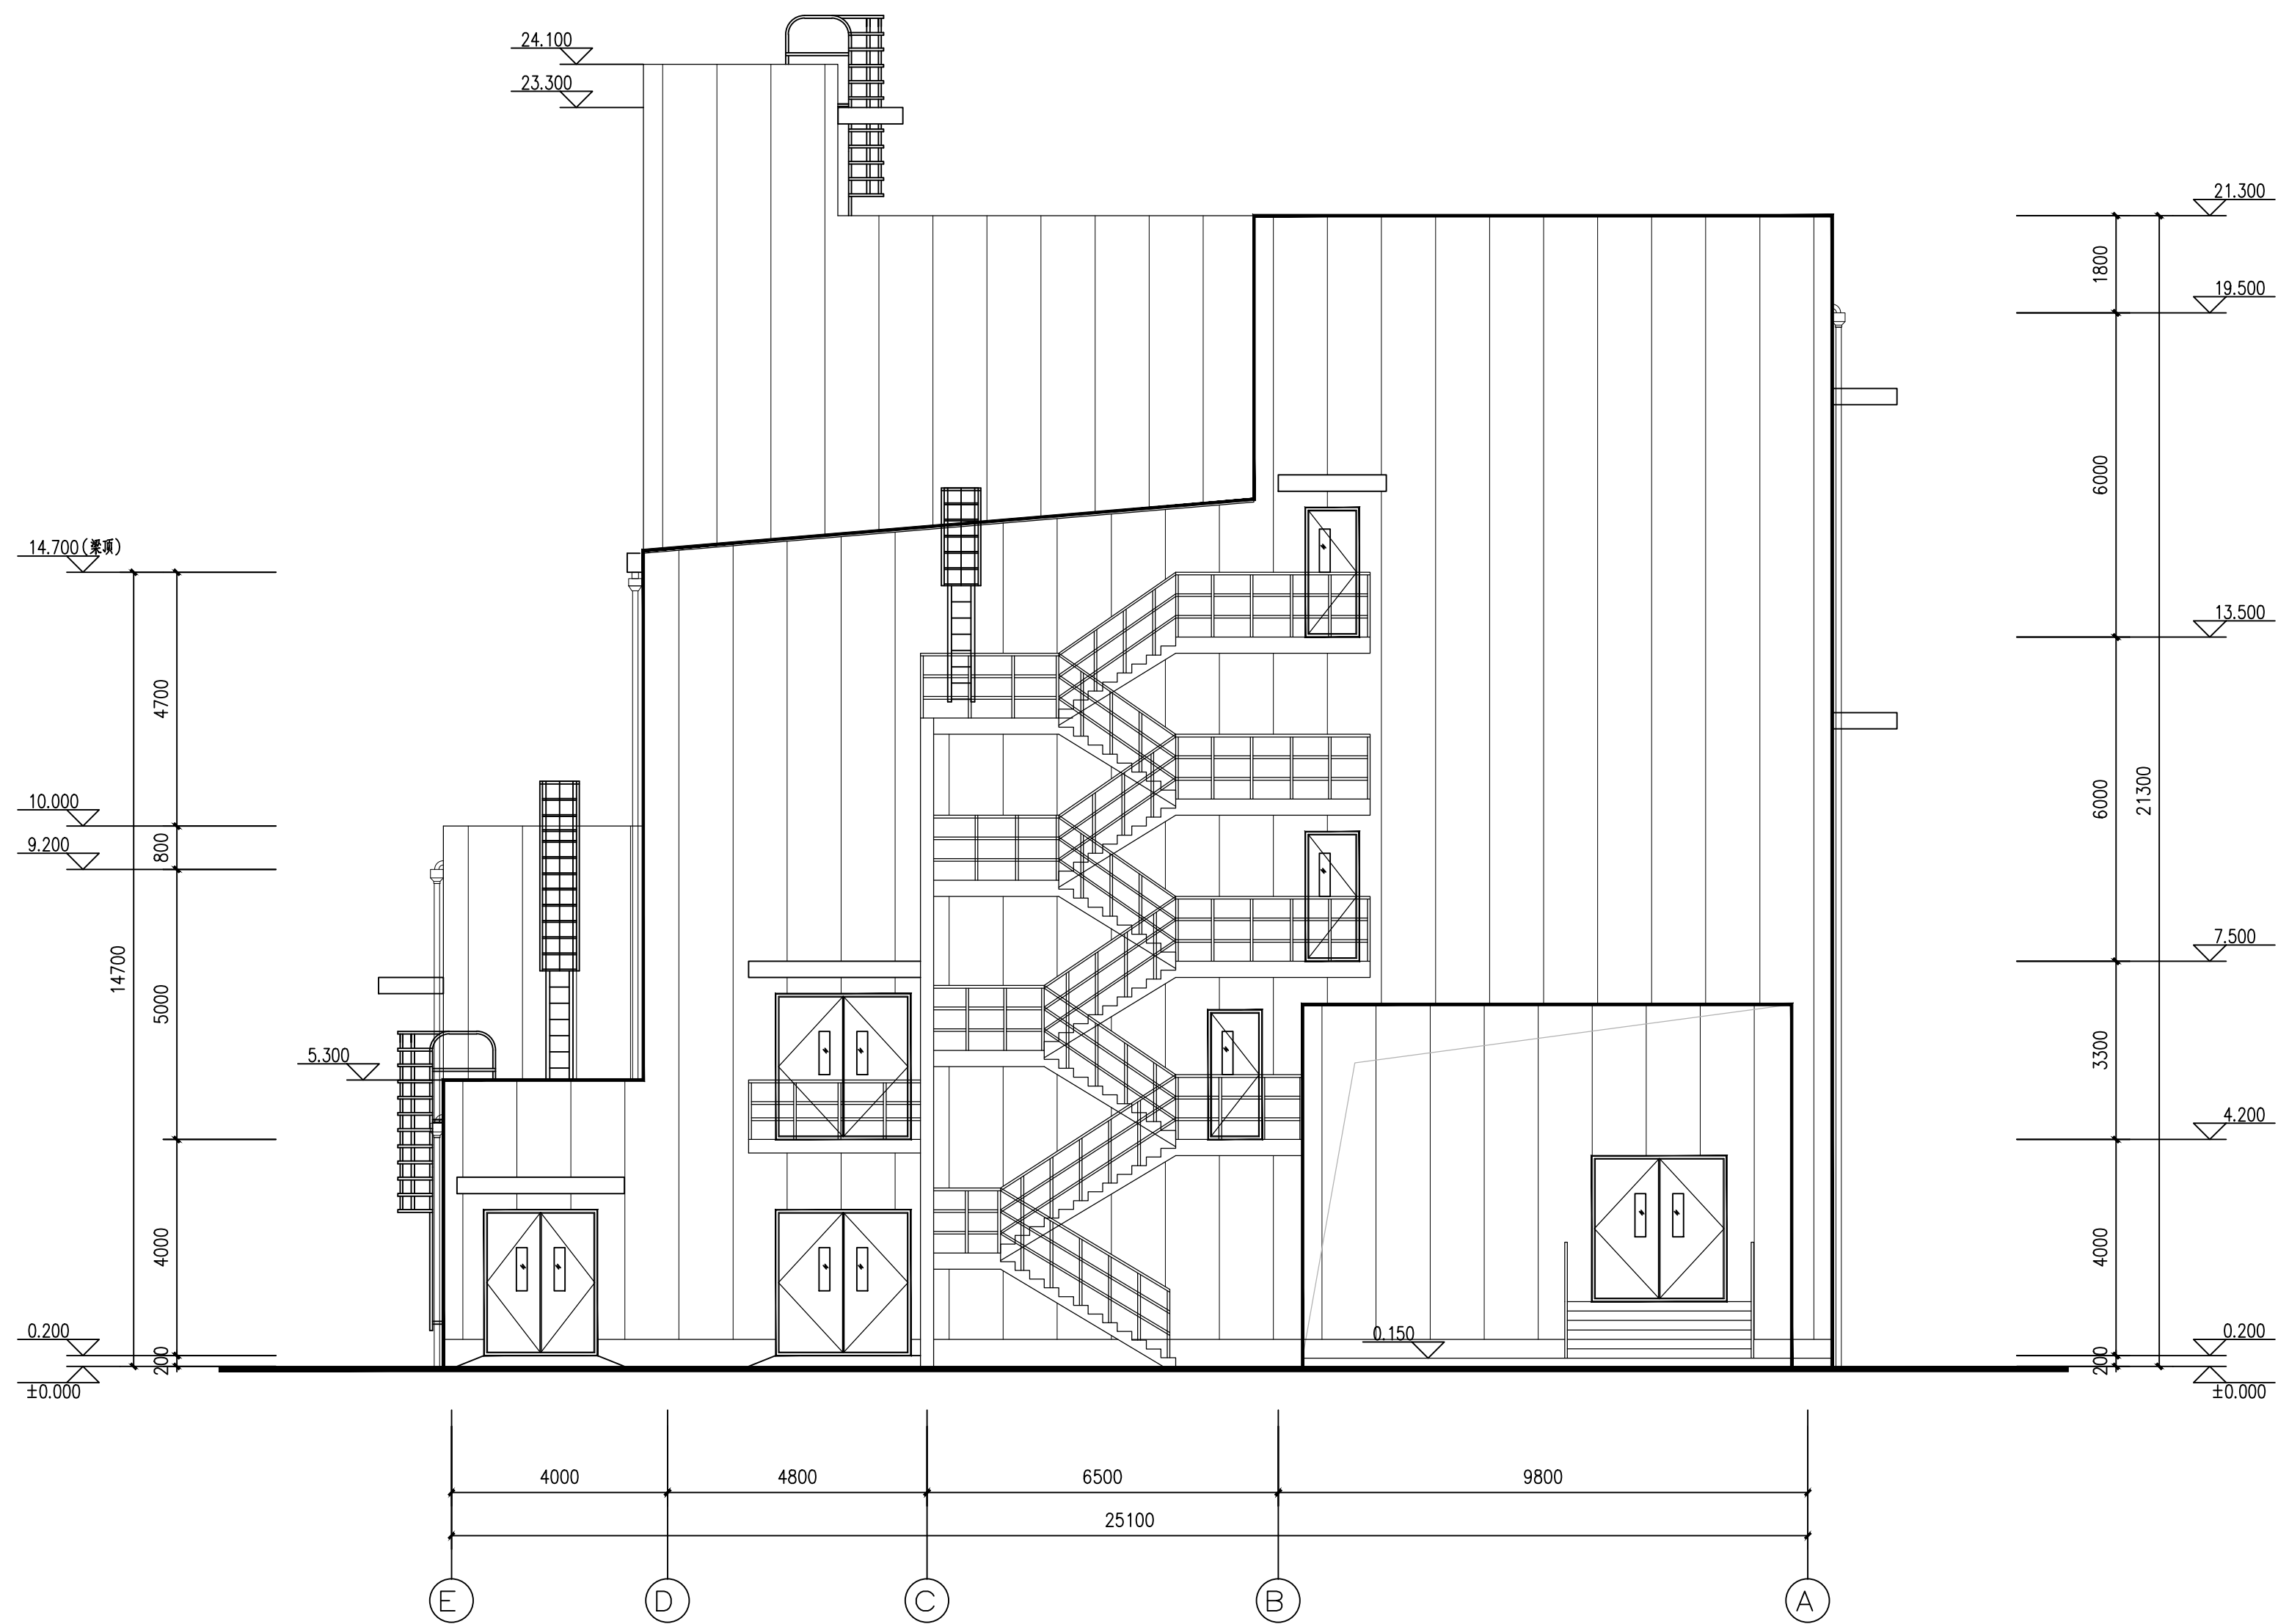

西立面图  
West Elevation 1:100

|                           |           |             |      |      |       |       |         |       |       |  |                                          |
|---------------------------|-----------|-------------|------|------|-------|-------|---------|-------|-------|--|------------------------------------------|
| SECURITY LEVEL<br>LEVEL-2 | REVISIONS |             |      |      |       |       | DATE    | 1/100 | MADE  |  | TITLE                                    |
|                           | No.       | DESCRIPTION | DATE | MADE | CH-KD | APP-D | JOB No. |       | APP-D |  | Manufacturing Building<br>West Elevation |
|                           |           |             |      |      |       |       |         |       |       |  | DWG. No.                                 |
|                           |           |             |      |      |       |       |         |       |       |  | ED-300-ARC-LAY-RCBG-0006                 |



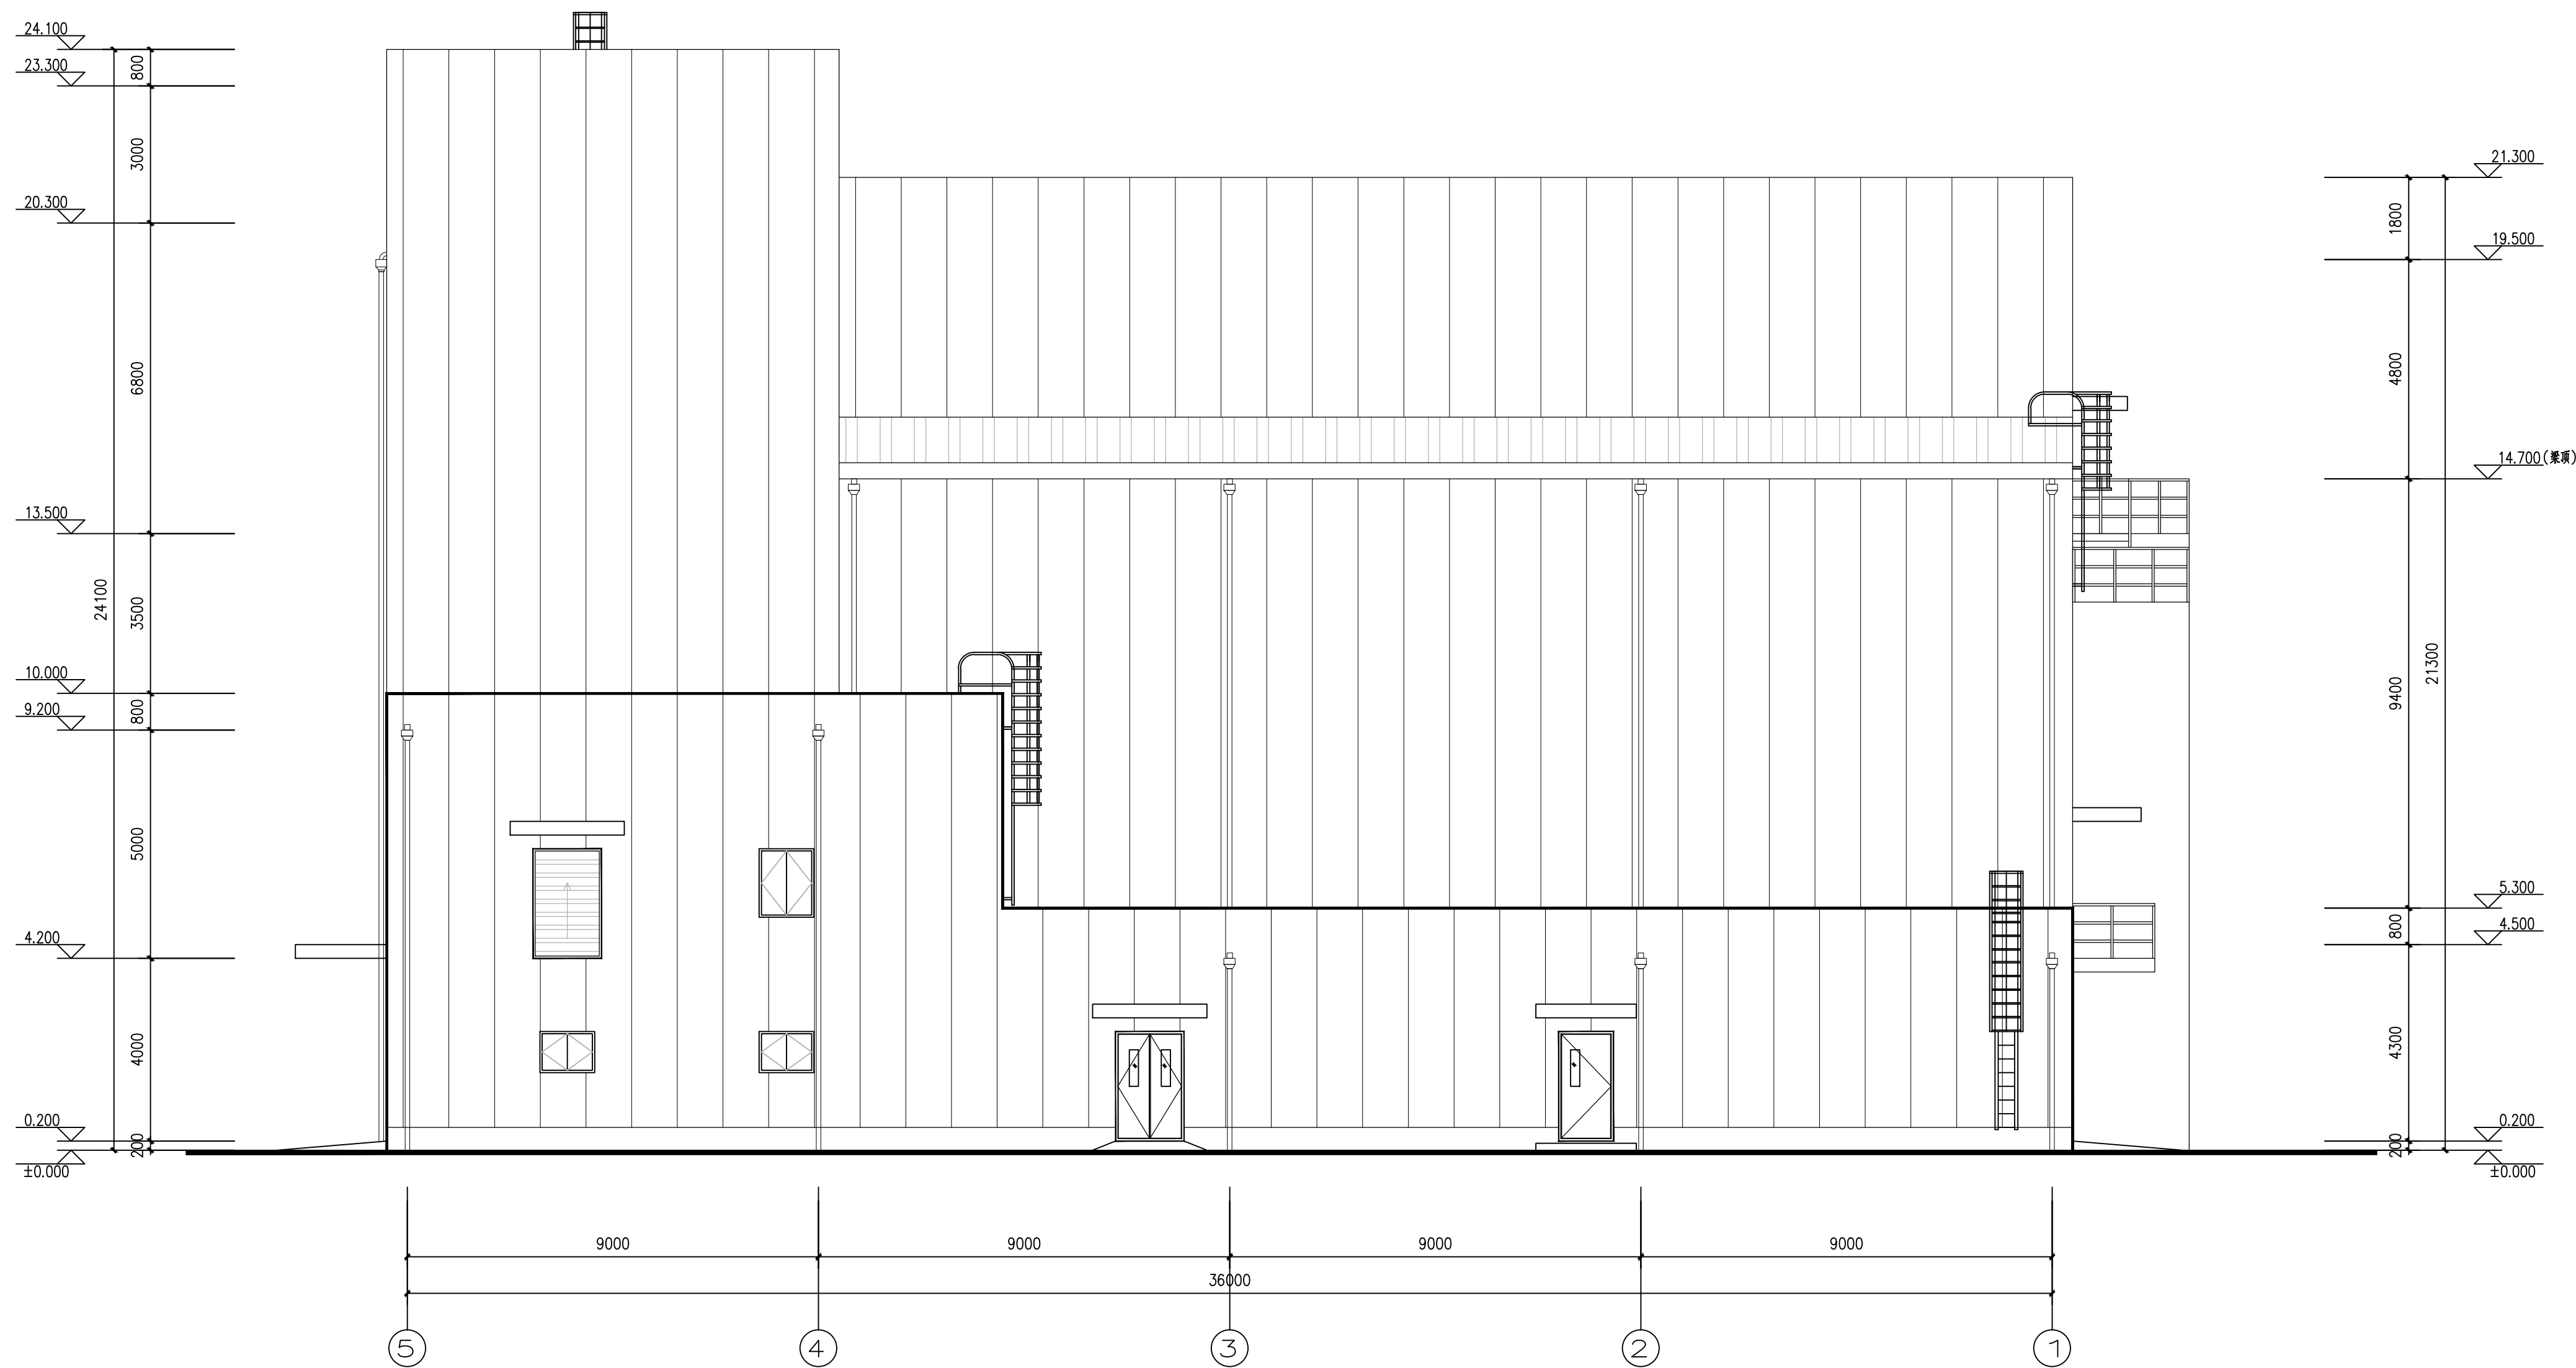

北立面图  
North Elevation

1:100

|                           |           |             |           |      |       |       |         |       |       |  |                        |                          |      |
|---------------------------|-----------|-------------|-----------|------|-------|-------|---------|-------|-------|--|------------------------|--------------------------|------|
| SECURITY LEVEL<br>LEVEL-2 |           |             |           |      |       |       | DATE    |       | MADE  |  | TITLE                  |                          |      |
|                           |           |             |           |      |       |       | SCALE   | 1/100 | CH*KD |  | Manufacturing Building |                          |      |
|                           |           |             |           |      |       |       | JOB No. |       | APP*D |  | North Elevation        |                          |      |
|                           |           | BED PACKAGE | Apr/20/26 | L*Y  | Y/N   | DH    |         |       |       |  |                        |                          |      |
|                           | No.       | DESCRIPTION | DATE      | MADE | CH*KD | APP*D |         |       |       |  |                        | DWG. No.                 | REV. |
|                           | REVISIONS |             |           |      |       |       |         |       |       |  |                        | ED-300-ARC-LAY-RCBG-0007 |      |




洁净区，工作范围含土  
建、暖通、电气等

非洁净区，工作范围仅含  
暖通

非洁净区，不在洁净分包  
工作范围内

洁净门，在洁净分包范围  
内

- 图例 Legend
- 100mm 成品金属岩棉夹芯板  
100mm Steel Sandwich Panel with Rock Wool
- 240厚蒸压加气混凝土砌块+ 方钢(见结构)  
+100mm 成品金属岩棉夹芯板  
240mm Aerated Concrete Block+Square Steel  
(refer to C/S Drawing)+100mm Steel Sandwich  
Panel with Rock Wool
- 240厚蒸压加气混凝土砌块  
240mm Aerated Concrete Block
- 防火隔墙，耐火极限不小于3h：240厚蒸压加气混凝土砌块  
Fire Partition Wall, Fire Resistance no less than 3h  
240mm Aerated Concrete Block
- 防爆防火墙，耐火极限不小于4h：  
240厚混凝土实心砖配筋  
Reinforced Fire Wall, Fire Resistance no less than 4h  
240mm Reinforced Solid Concrete Brick
- 穿孔吸音石膏板内填玻璃棉  
Perforated Acoustic Gypsum Board with Glass Wool
- 洁净板  
Clean Board

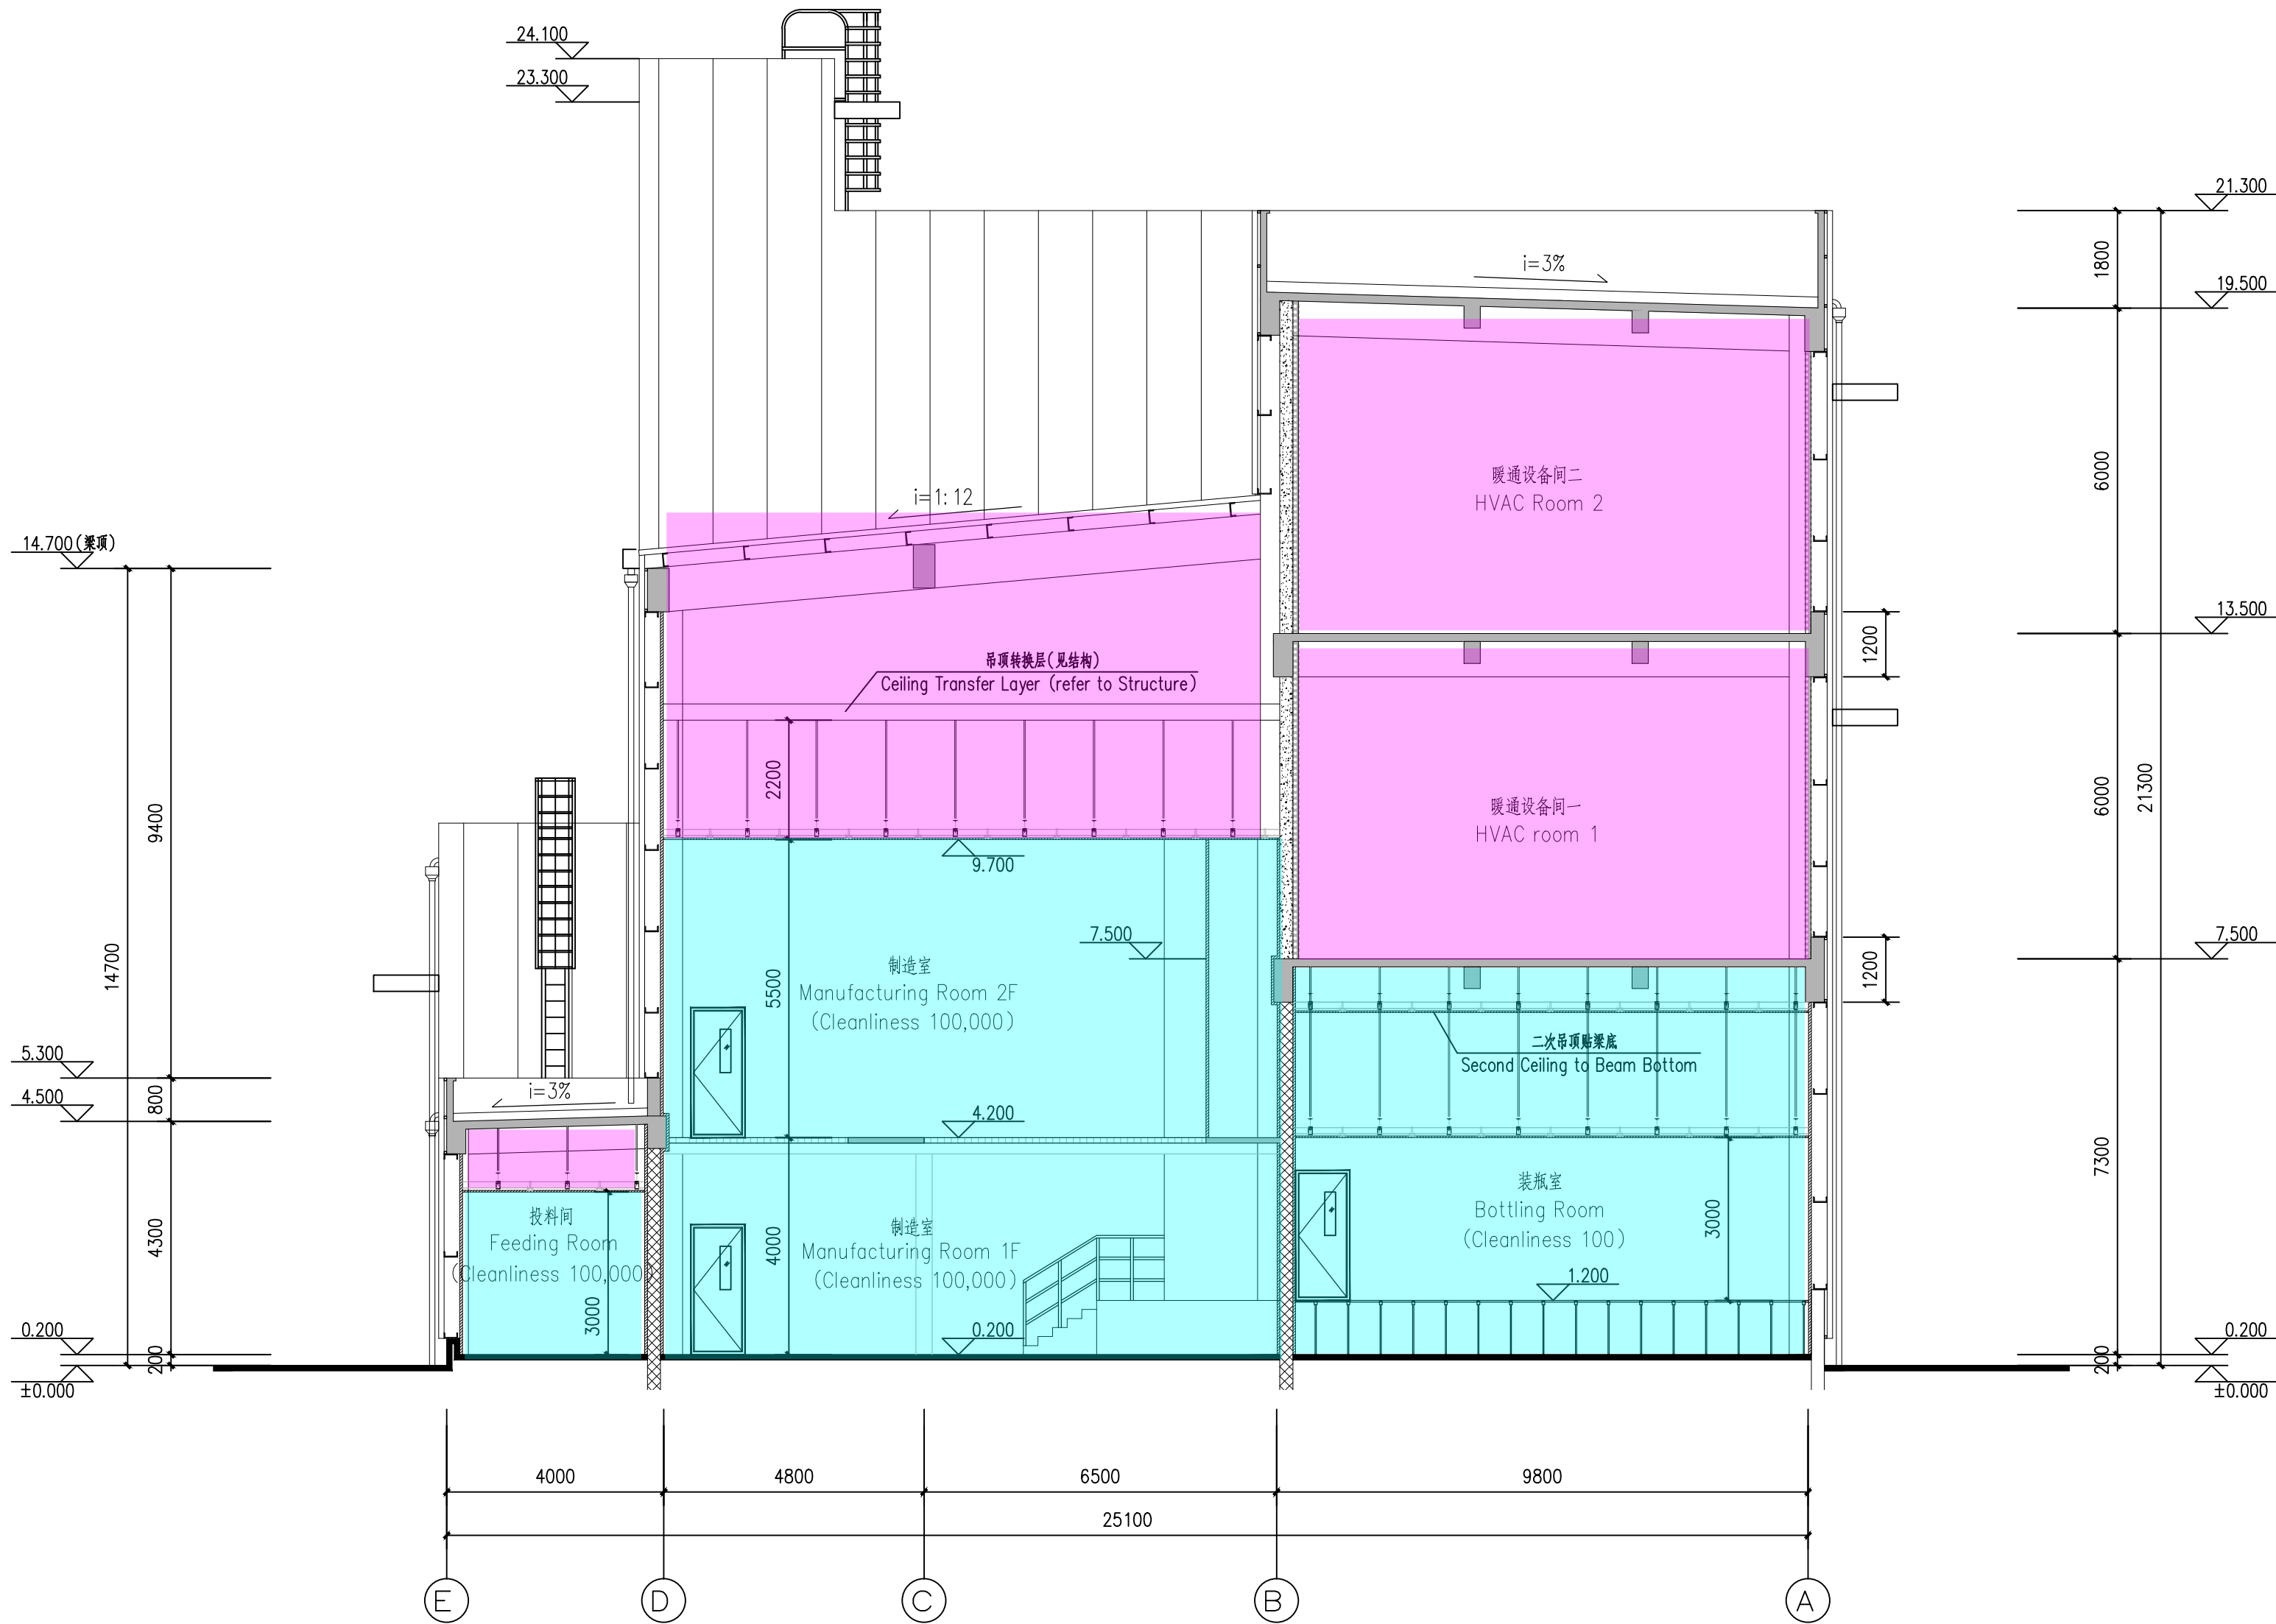

1-1 剖面图  
1-1 Section  
1:100

|                           |           |             |      |      |       |          |       |       |                        |
|---------------------------|-----------|-------------|------|------|-------|----------|-------|-------|------------------------|
| SECURITY LEVEL<br>LEVEL-2 | REVISIONS |             |      |      |       | DATE     | SCALE | MAGE  | TITLE                  |
|                           | No.       | DESCRIPTION | DATE | MADE | CH·KD | APP·D    | 1/100 | CH·KD | Manufacturing Building |
|                           |           |             |      |      |       | JOB No.  |       | APP·D | 1-1 Section            |
|                           |           |             |      |      |       | DWC. No. |       |       | REV.                   |

ED-300-ARC-LAY-RCBG-0008

0